

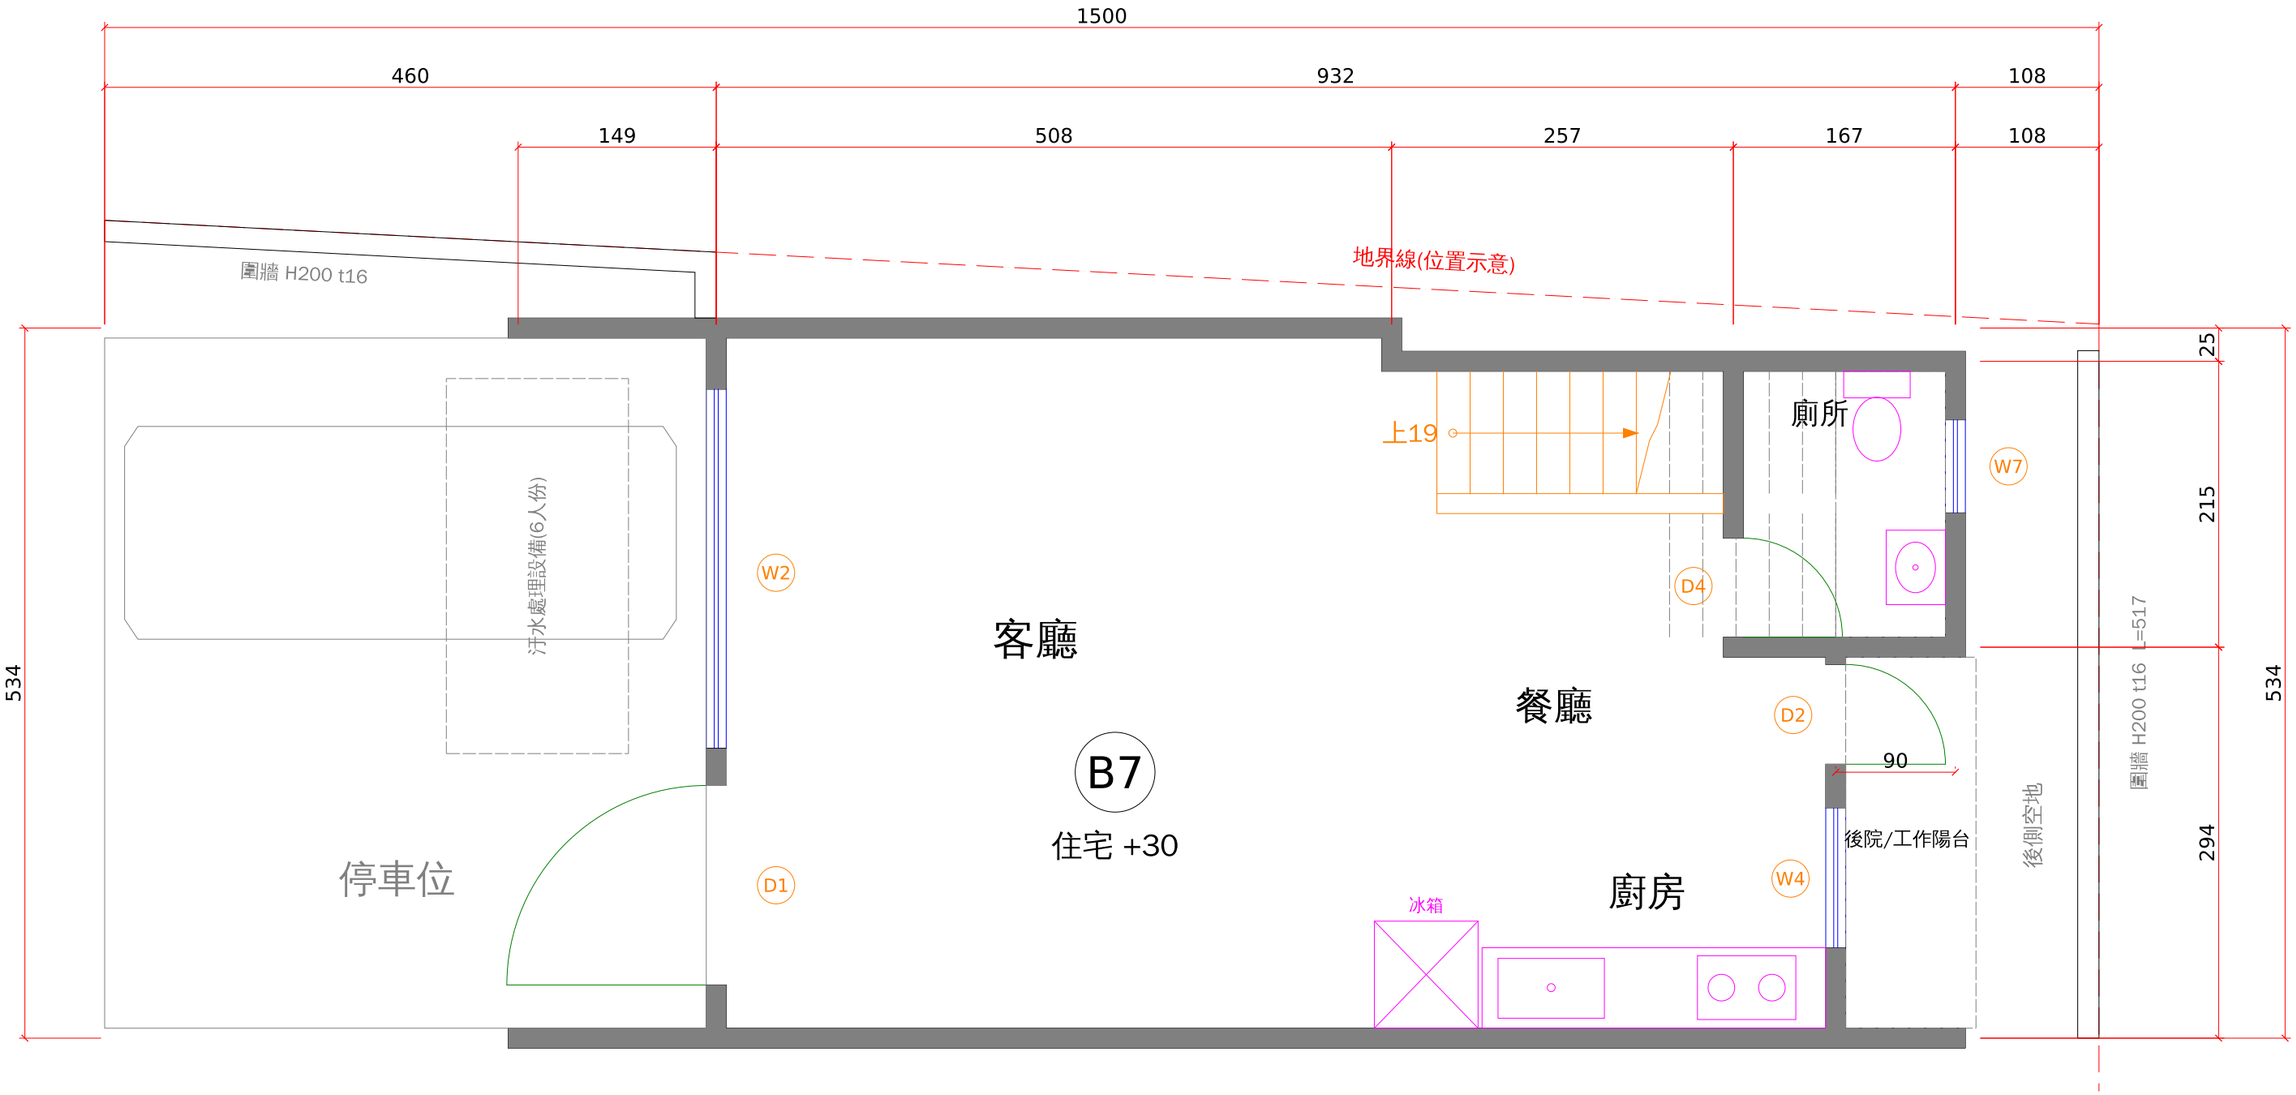


B7 一層平面圖　S=1/50

B7戶 平面圖 rev.2（依原圖照片判讀重繪，非原始CAD）
1. 單位：cm。尺寸鍊均為牆中心線（依原圖）；原圖無標註者依圖面比例量取。
2. 外牆、分戶牆、隔間牆、女兒牆厚度均為15。
3. 北側外牆於X=968處退縮25：X968以西中心線Y=534，以東中心線Y=509（即右側尺寸鍊25/215/294）。
4. 西側外牆：1F中心線X=460（149=311→460），2F/3F中心線X=441（130=311→441），二三樓外牆較一樓外推19。
5. 高程：GL±0、1FL+30、2FL+390、3FL+710、RFL+1030；1F層高360、2F/3F層高320；女兒牆頂約+1170。
6. 樓梯：1F→2F 19級@18.95=360；2F→3F 17級@18.82=320；踏面25（依圖面比例）；梯寬約92。
7. 結構柱未繪（柱尺寸照片無法判讀）。門窗寬度依圖面比例量取，請以門窗表核對。

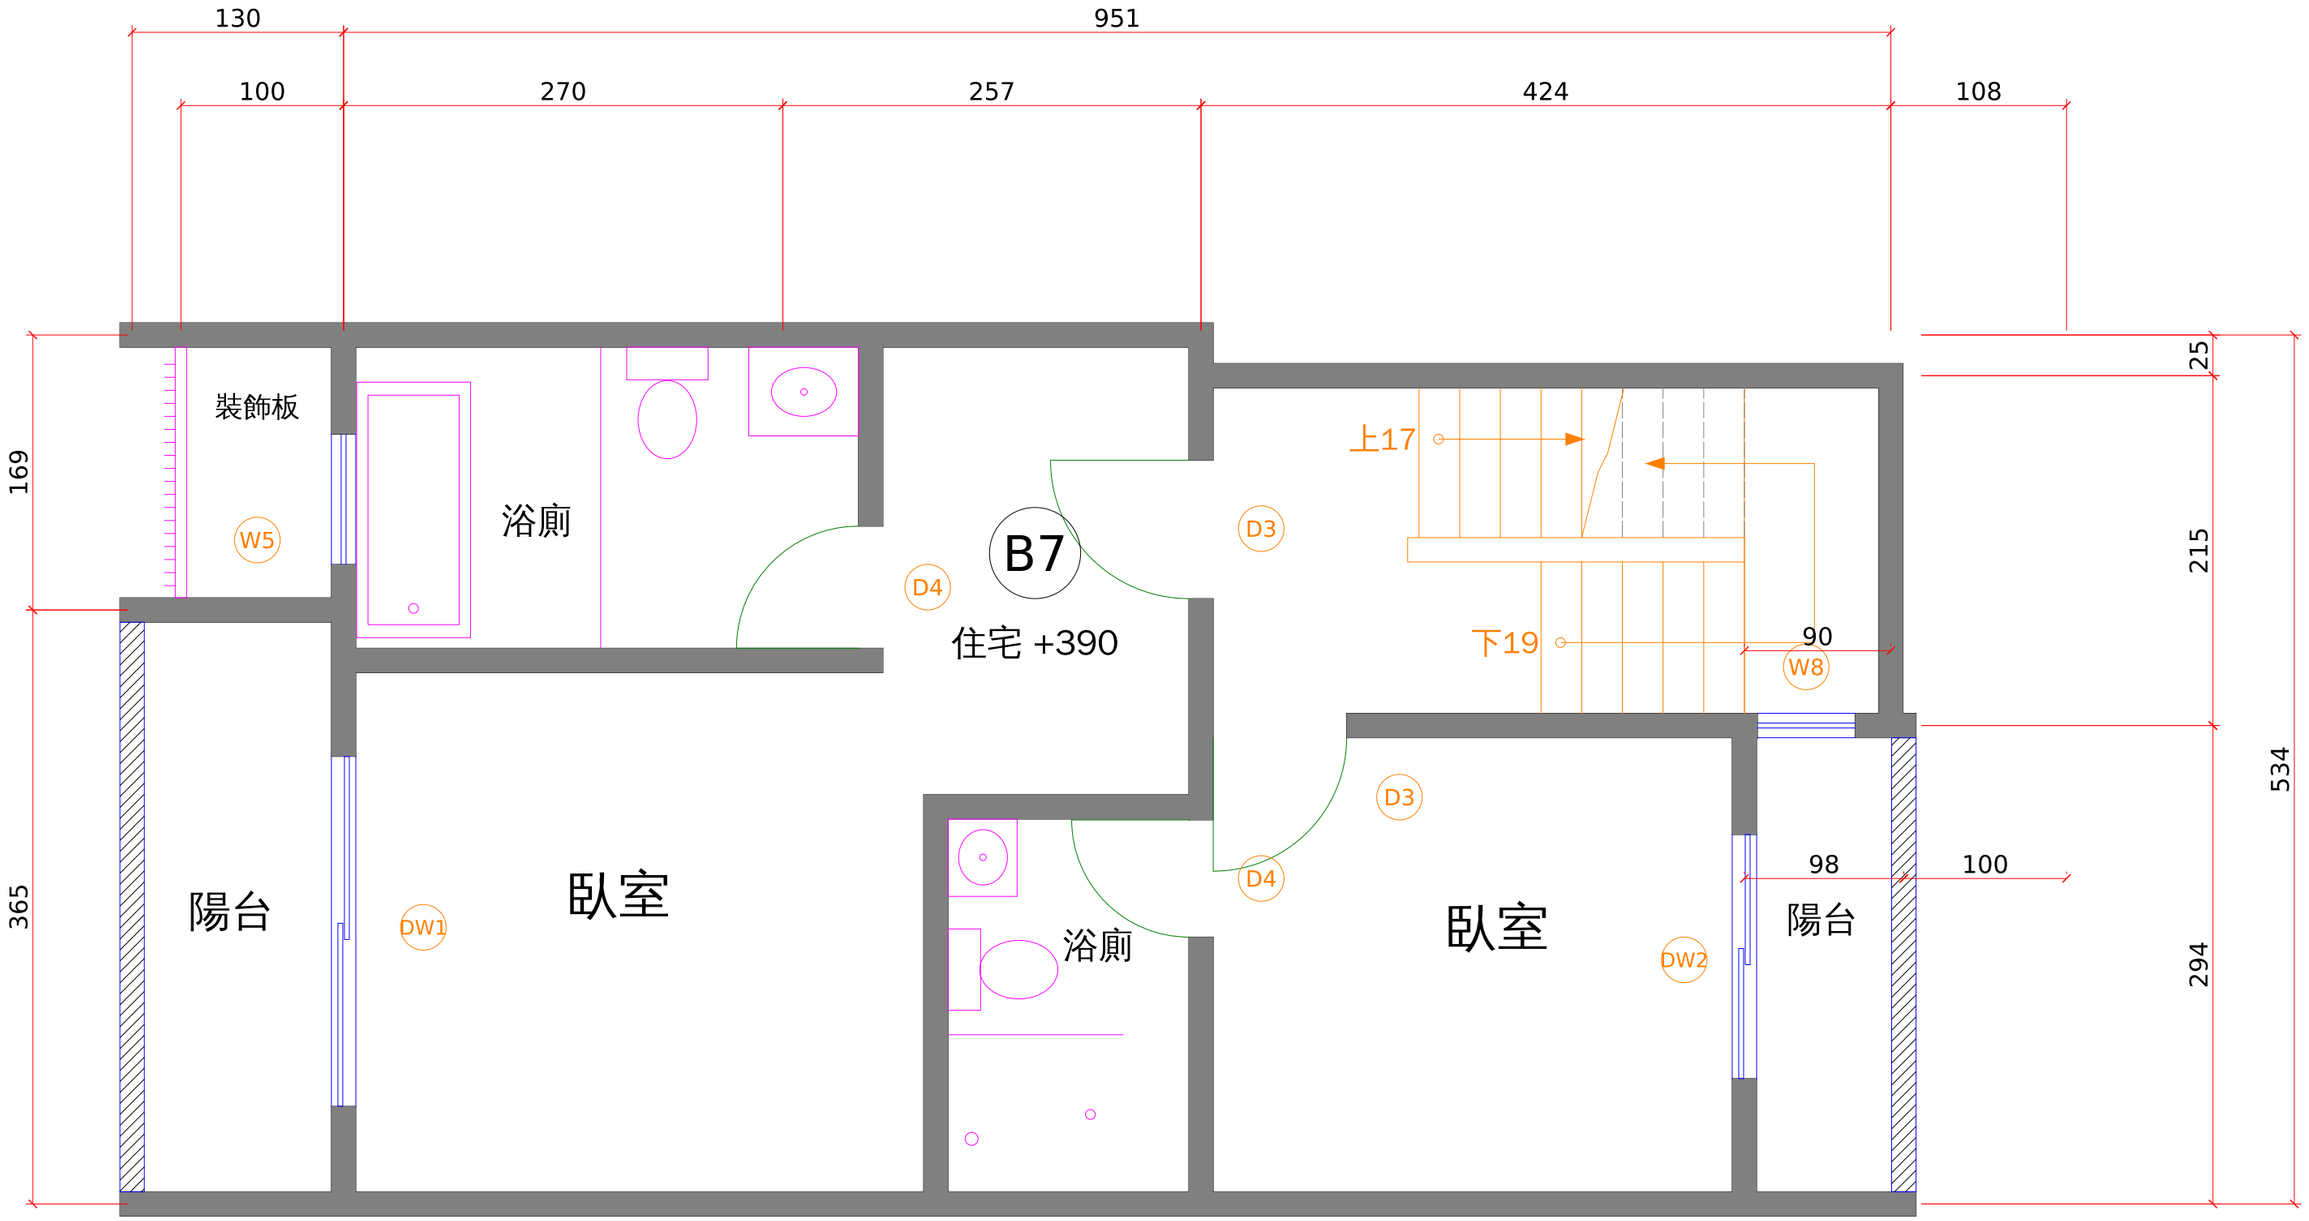

B7 二層平面圖　S=1/50

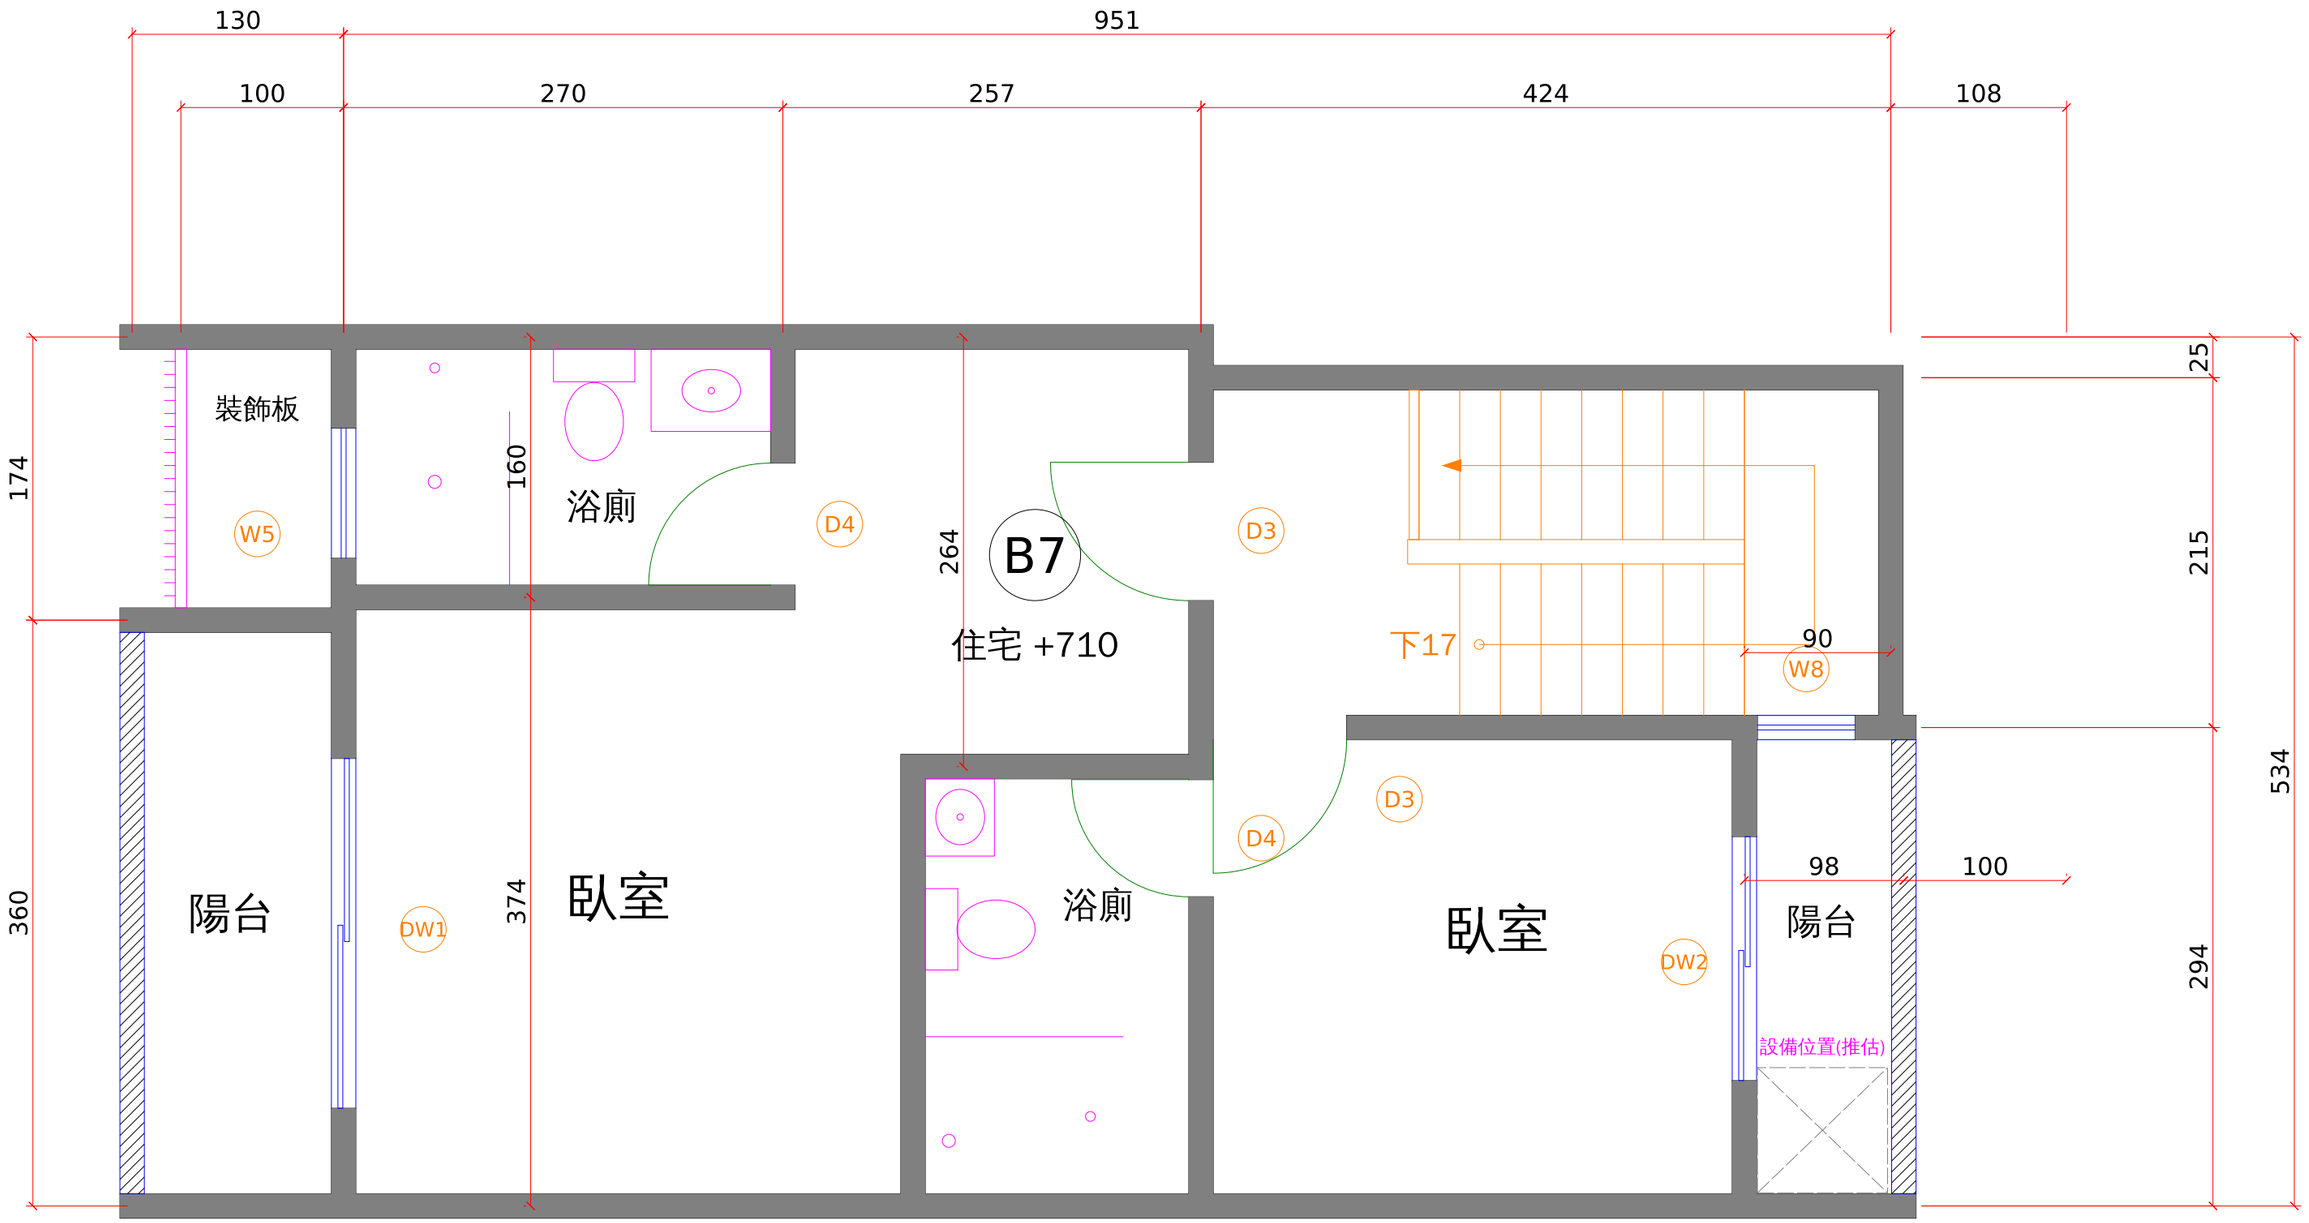

B7 三層平面圖　S=1/50