

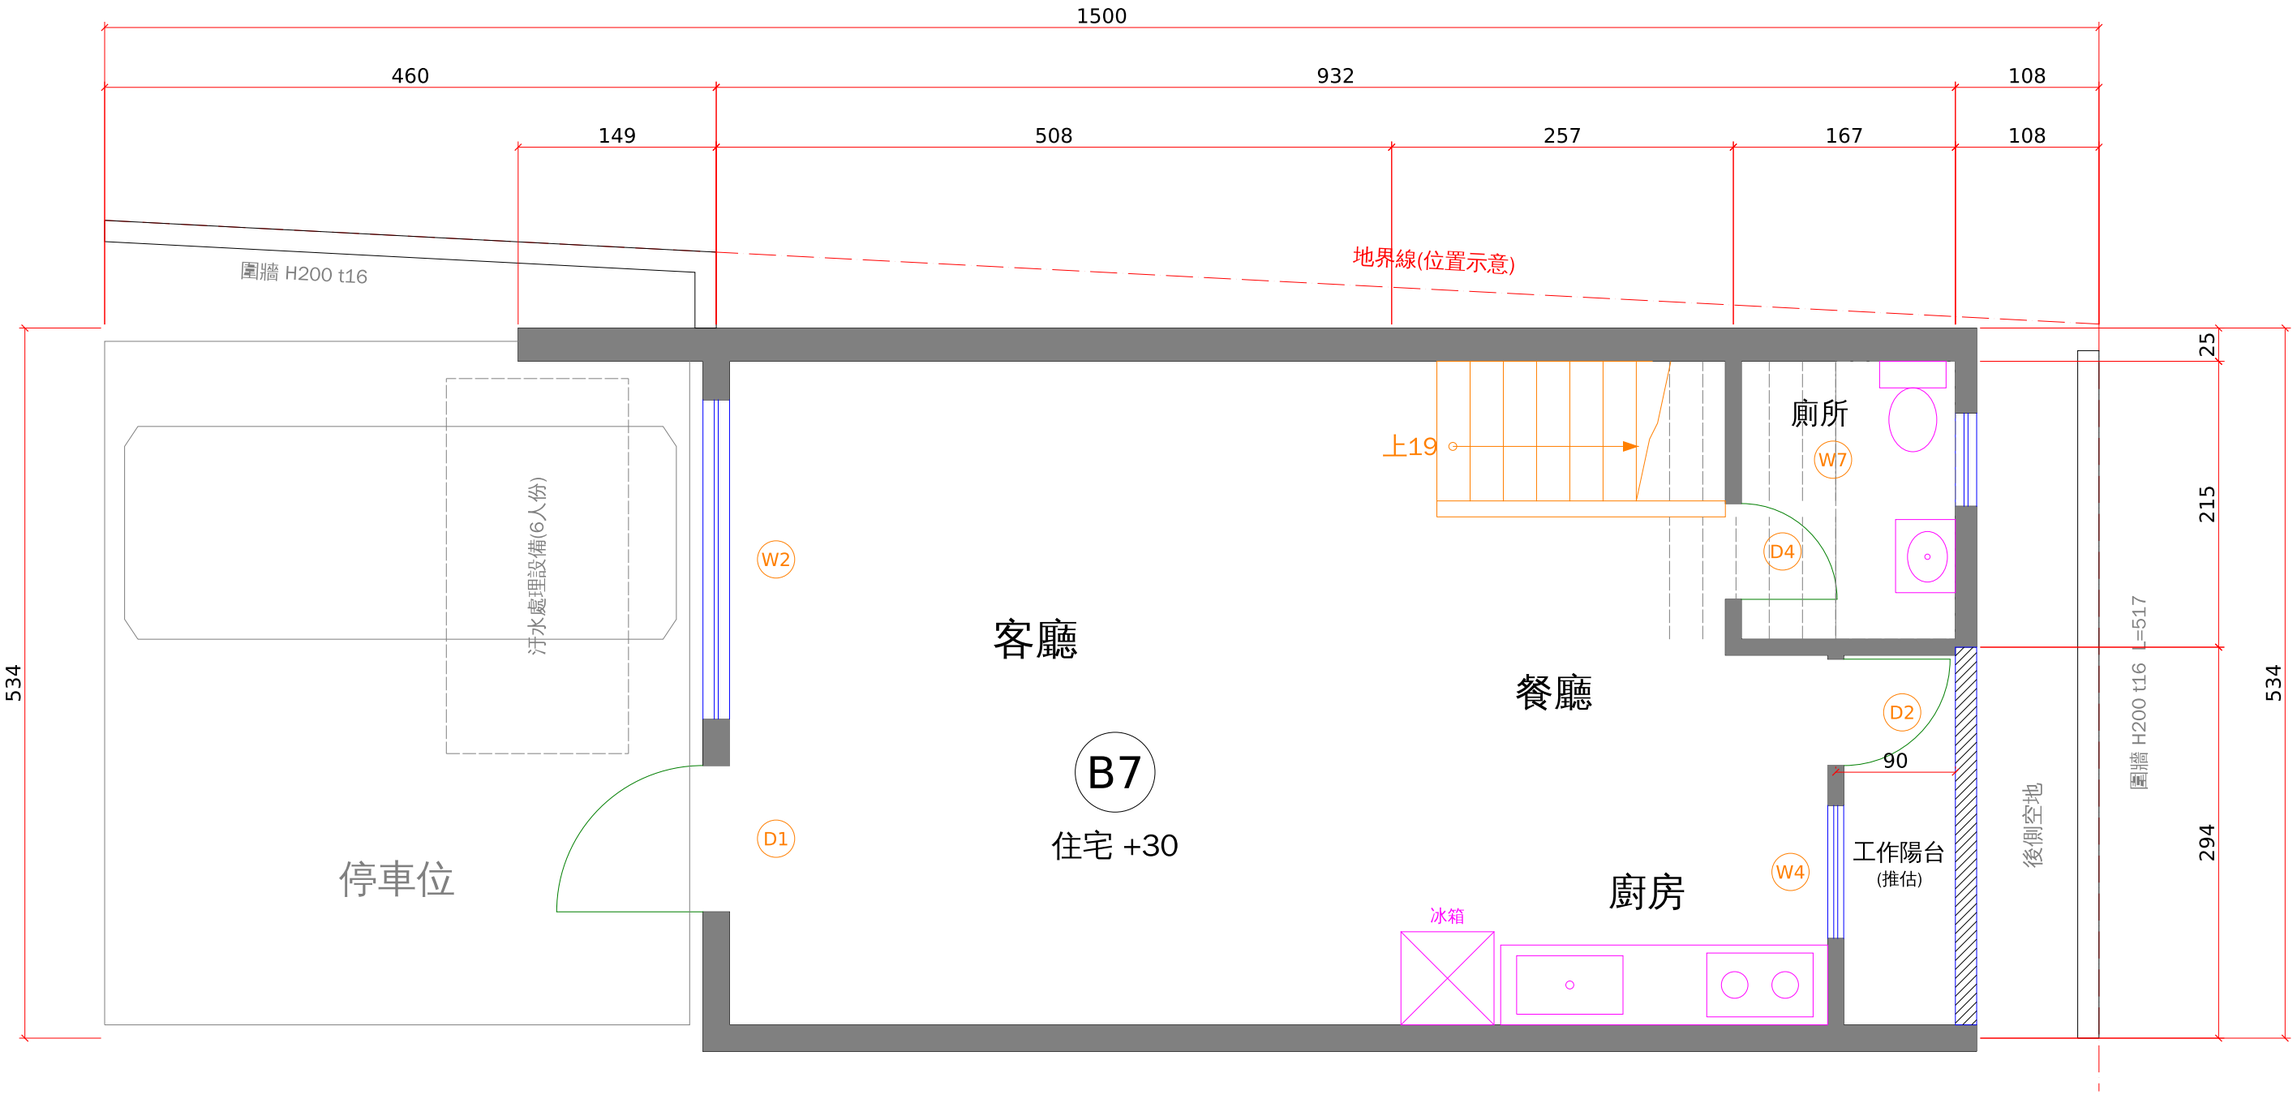


B7 一層平面圖　S=1/50

B7戶 平面圖（依原圖照片判讀重繪，非原始CAD）
1. 單位：cm。尺寸鍊數值依原圖標註；原圖無標註者依照片比例推估。
2. 牆厚假設：北側外牆25（外緣對齊尺寸線）；東側外牆/陽台女兒牆16（中心線X=1400）；西側外牆20（中心線 1F=460、2F/3F=441）；分戶牆20；室內隔間12（中心線）。
3. 高程（依剖面A3-11/12/13）：GL±0、1FL+30、2FL+390、3FL+710、RFL+1030、女兒牆頂約+1170。
4. 樓梯：1F→2F 19級@18.95=360；2F→3F 17級@18.82=320；踏面推估25；扶手高90。陽台欄杆高110。
5. 結構柱、梁未繪（照片解析度不足），請依結構圖補繪。門窗寬度為推估，請依門窗表修正。
6. 2F浴廁(含浴缸)東牆X=765、3F浴廁東牆X=711，兩層不同，依照片判讀，請確認。

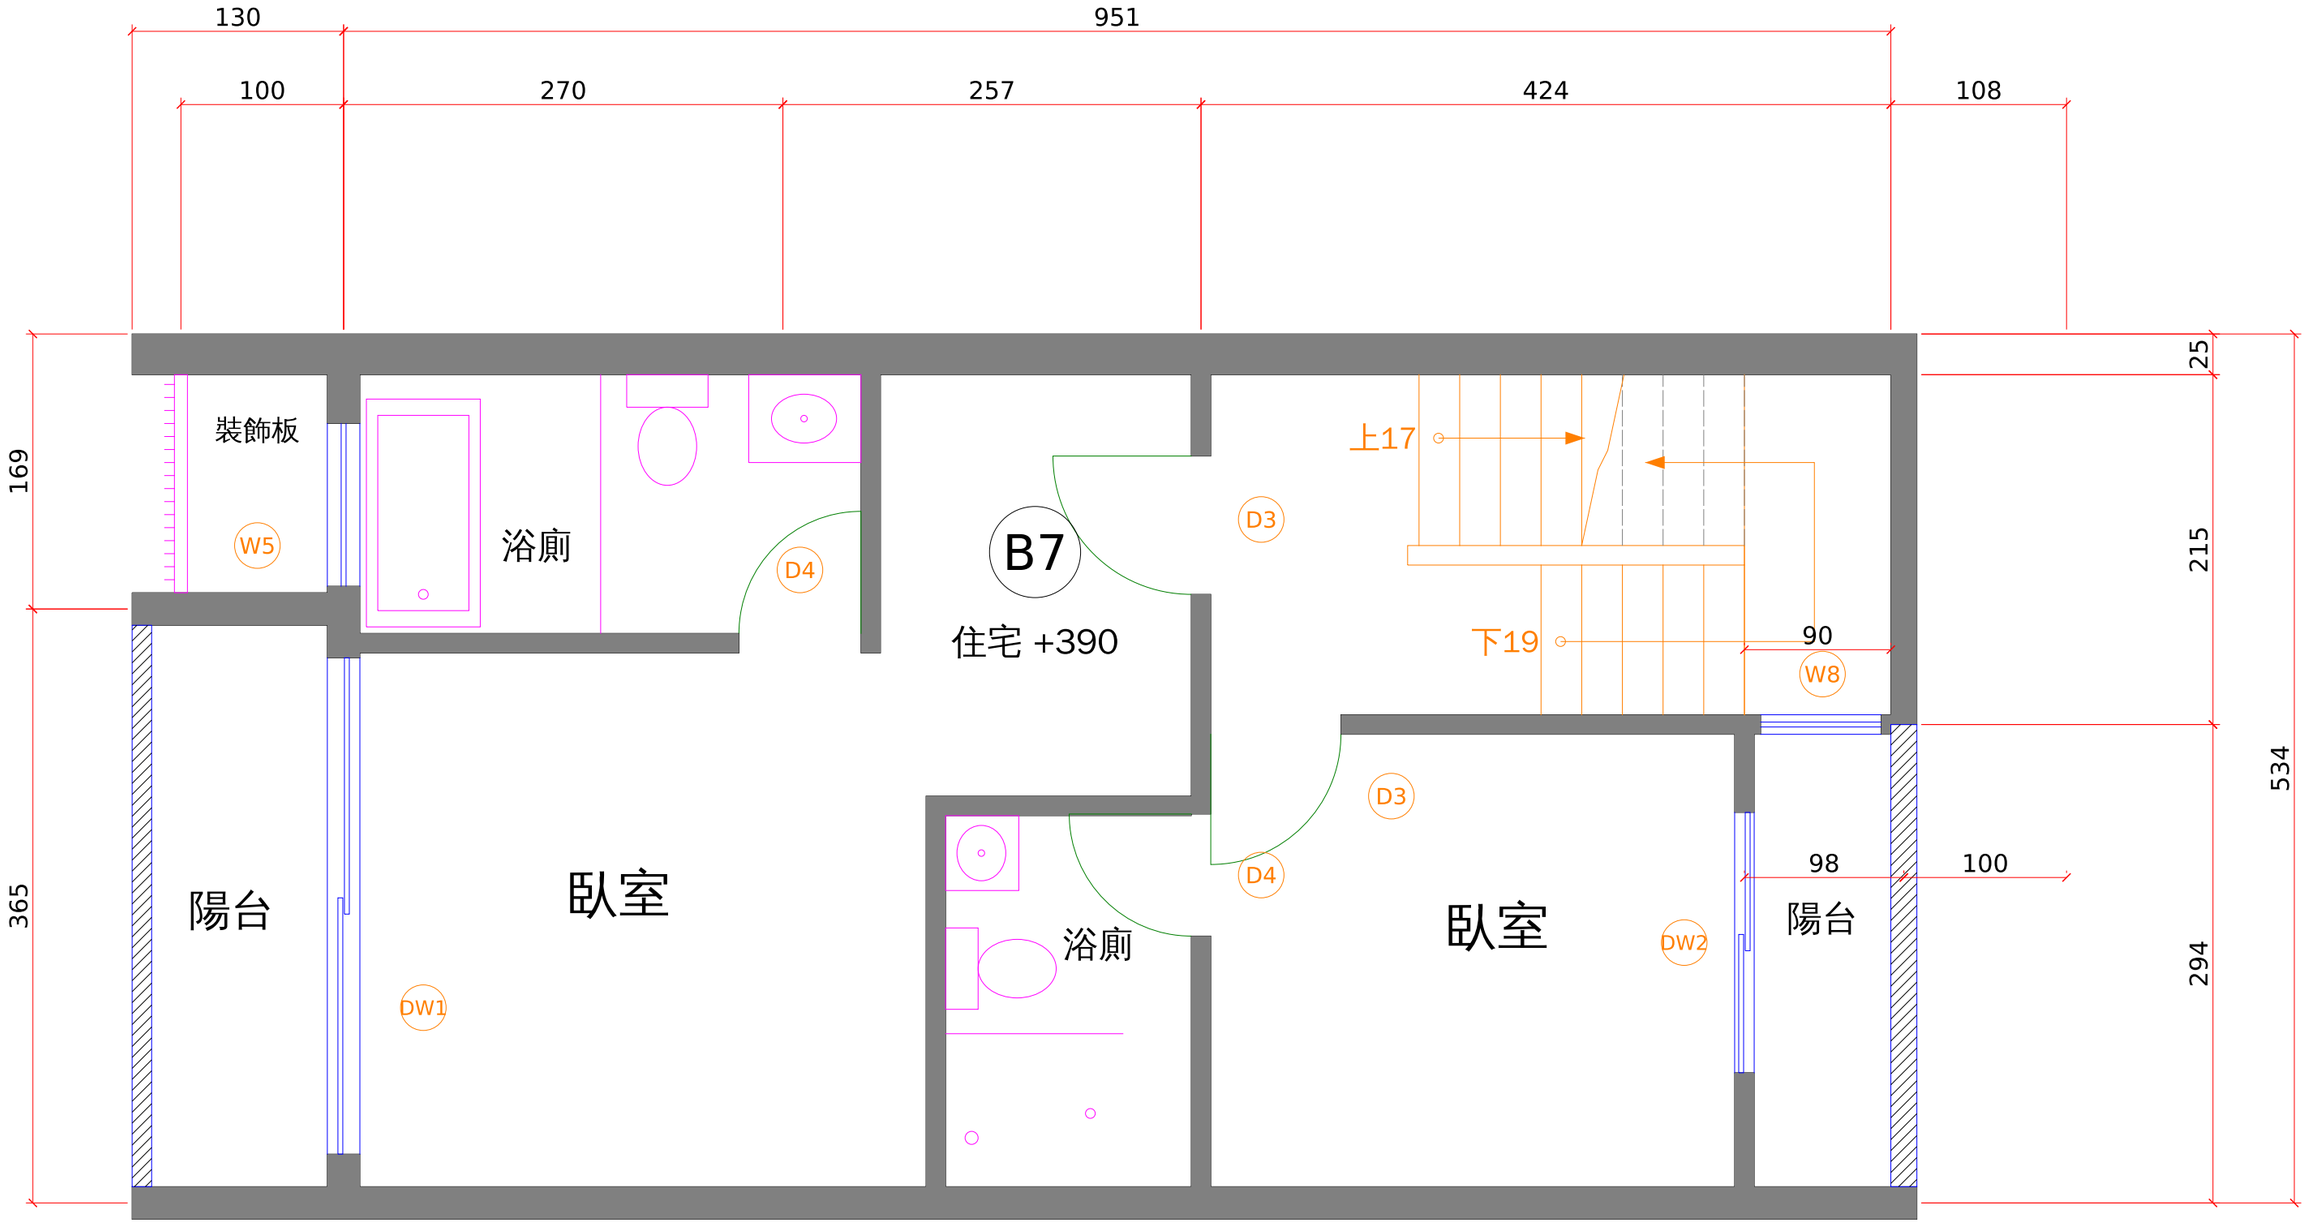

B7 二層平面圖　S=1/50

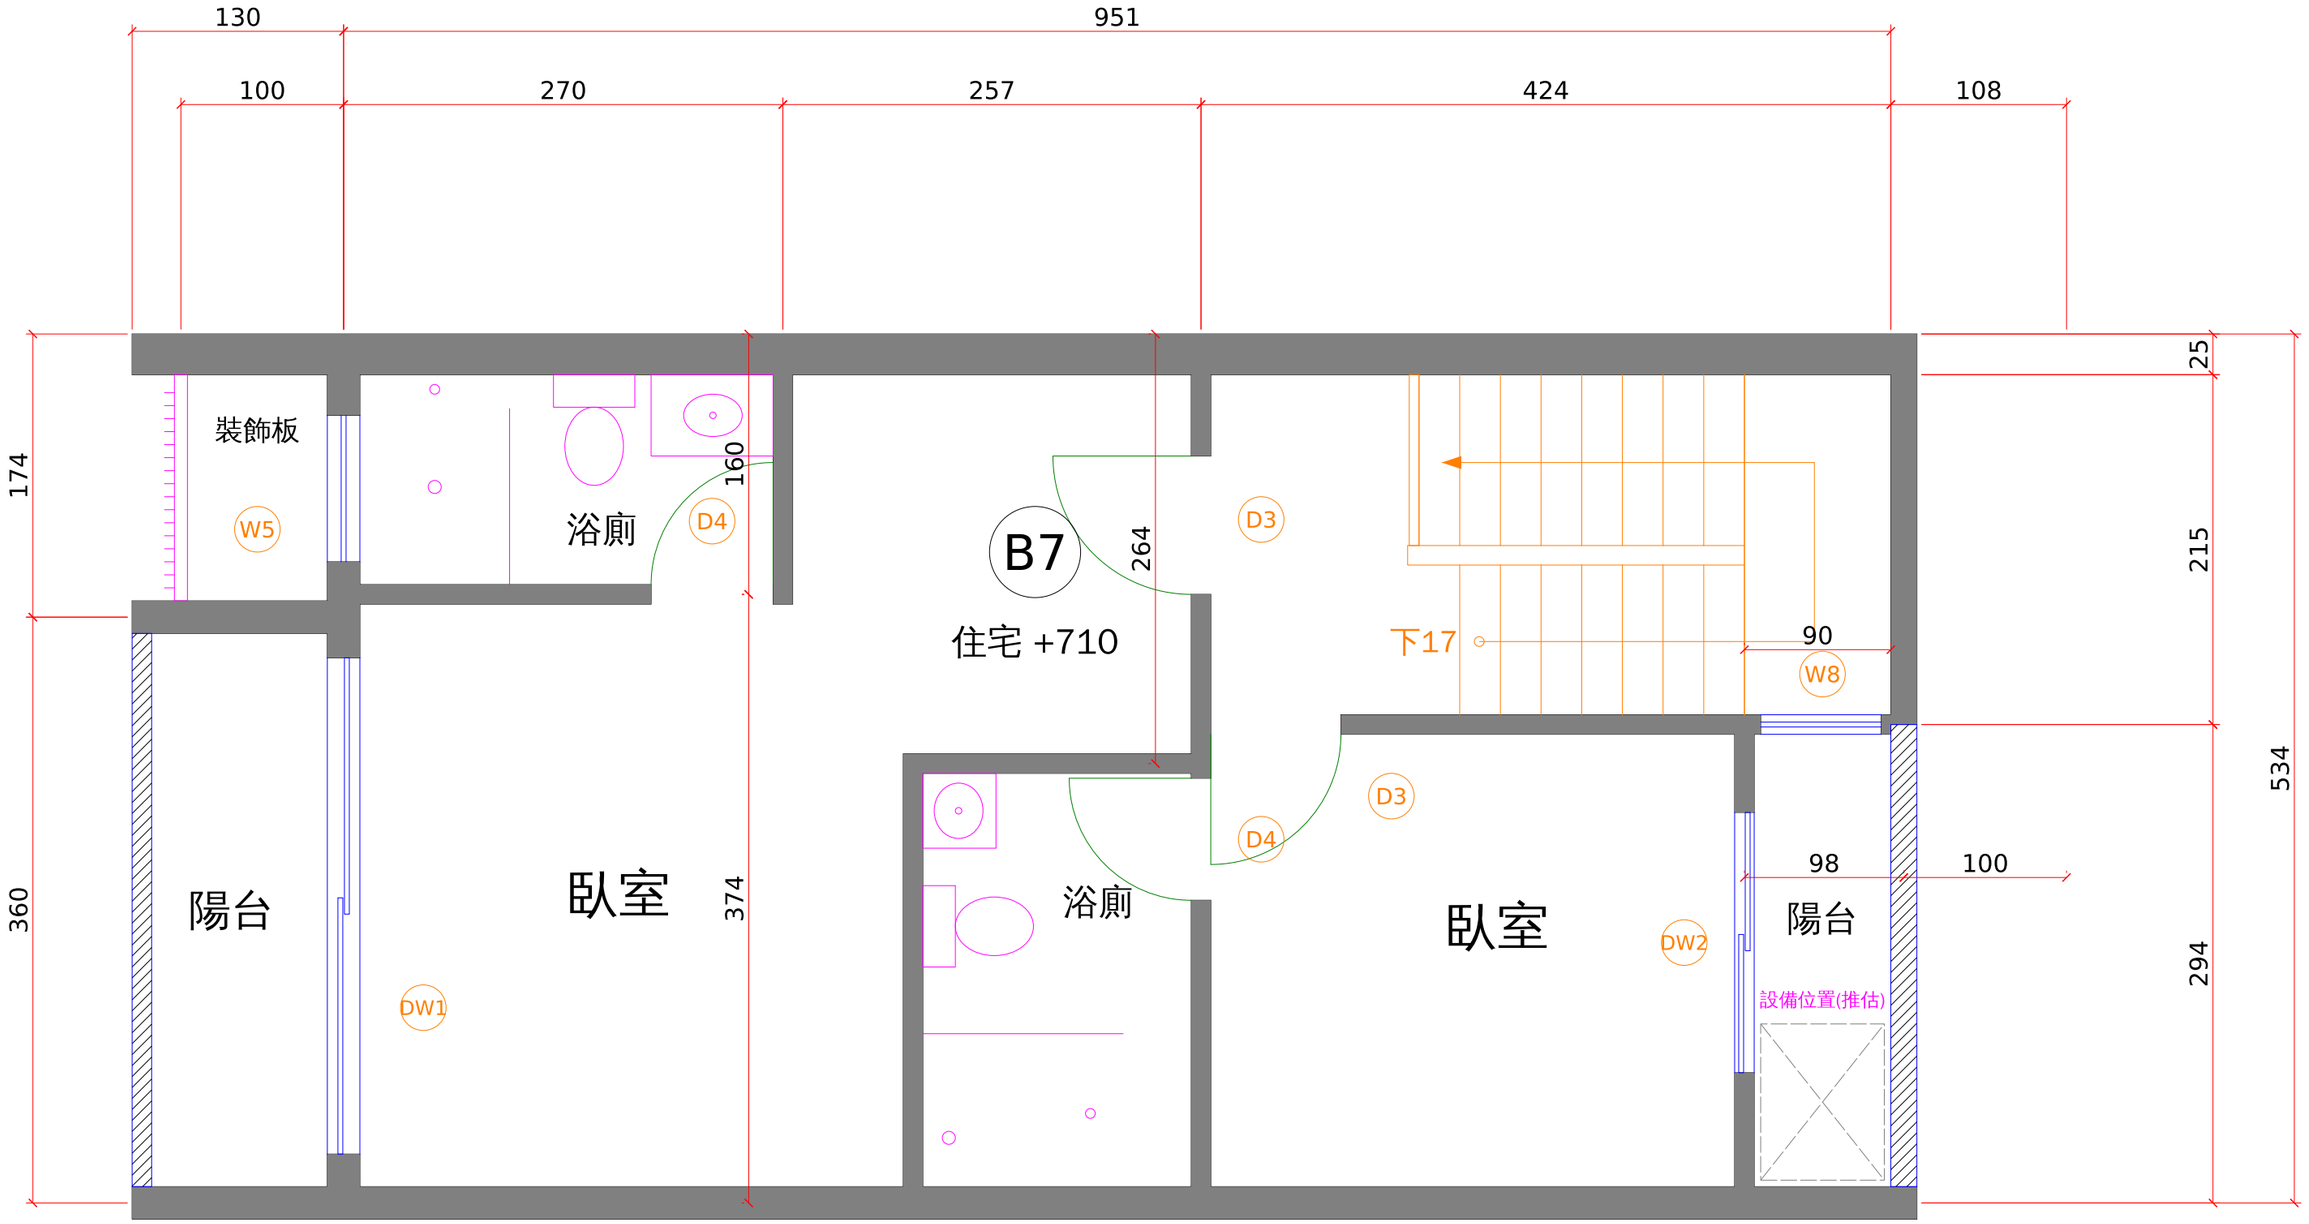

B7 三層平面圖　S=1/50