
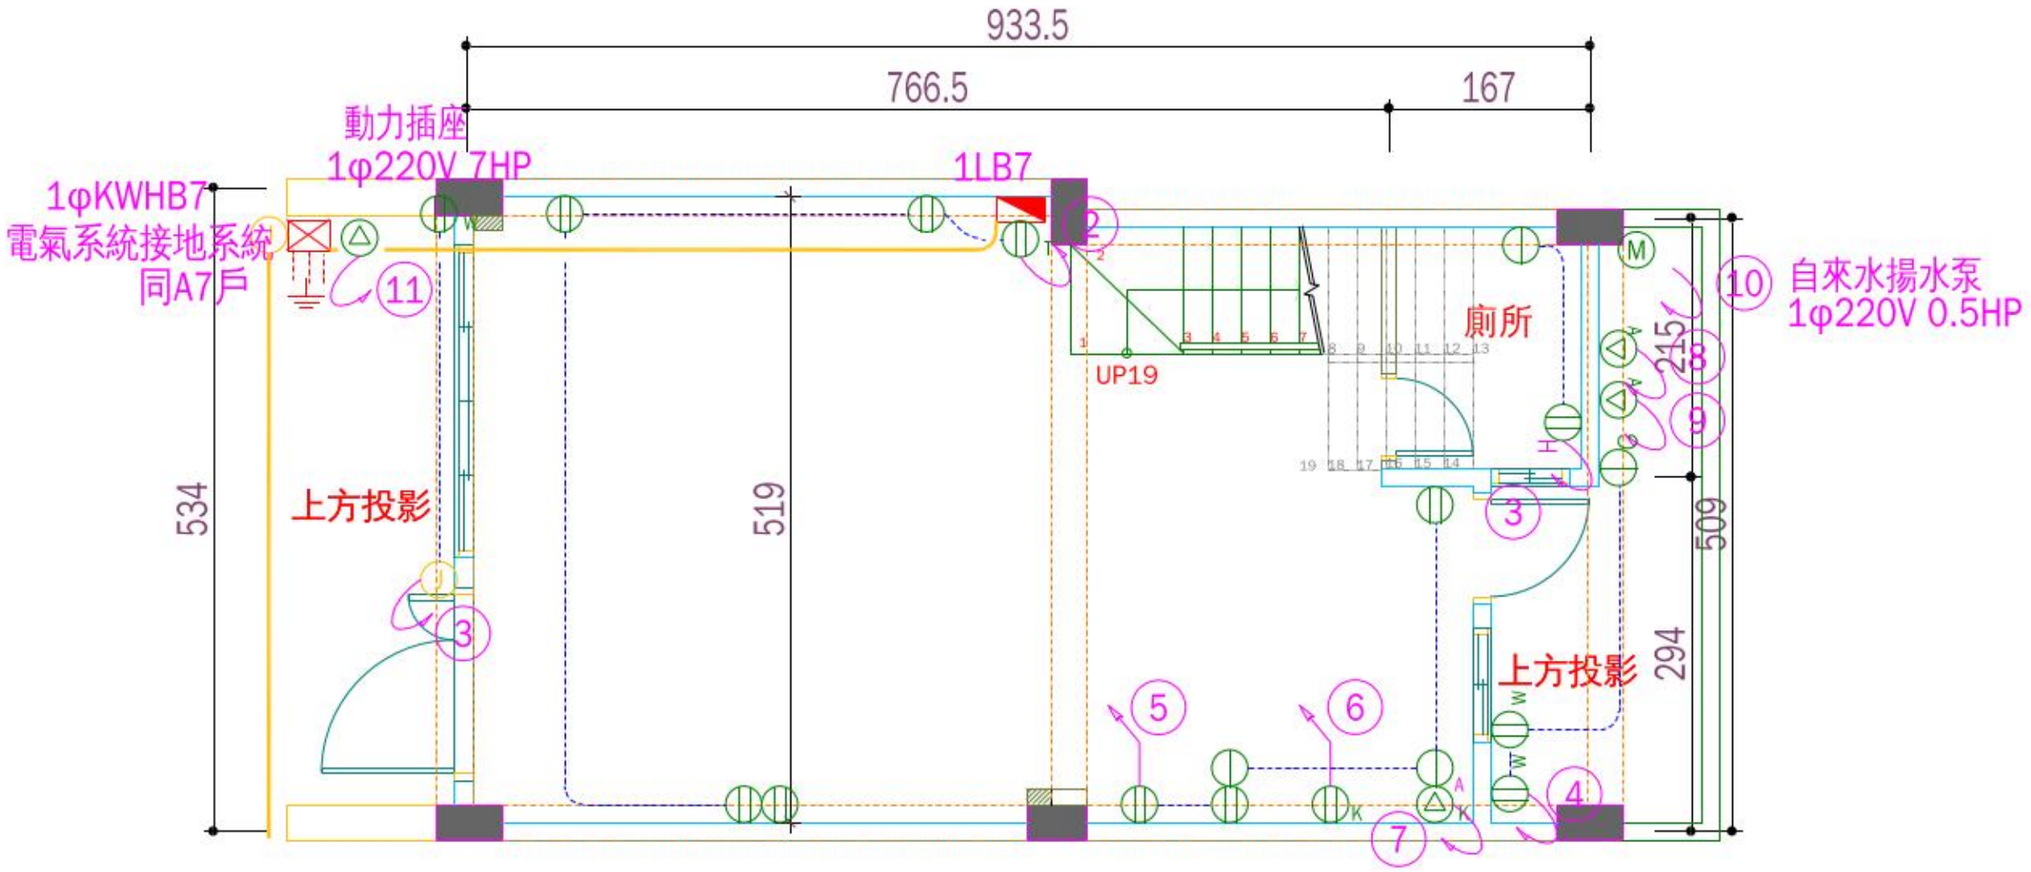



1F插座設備配置圖

S=1/100

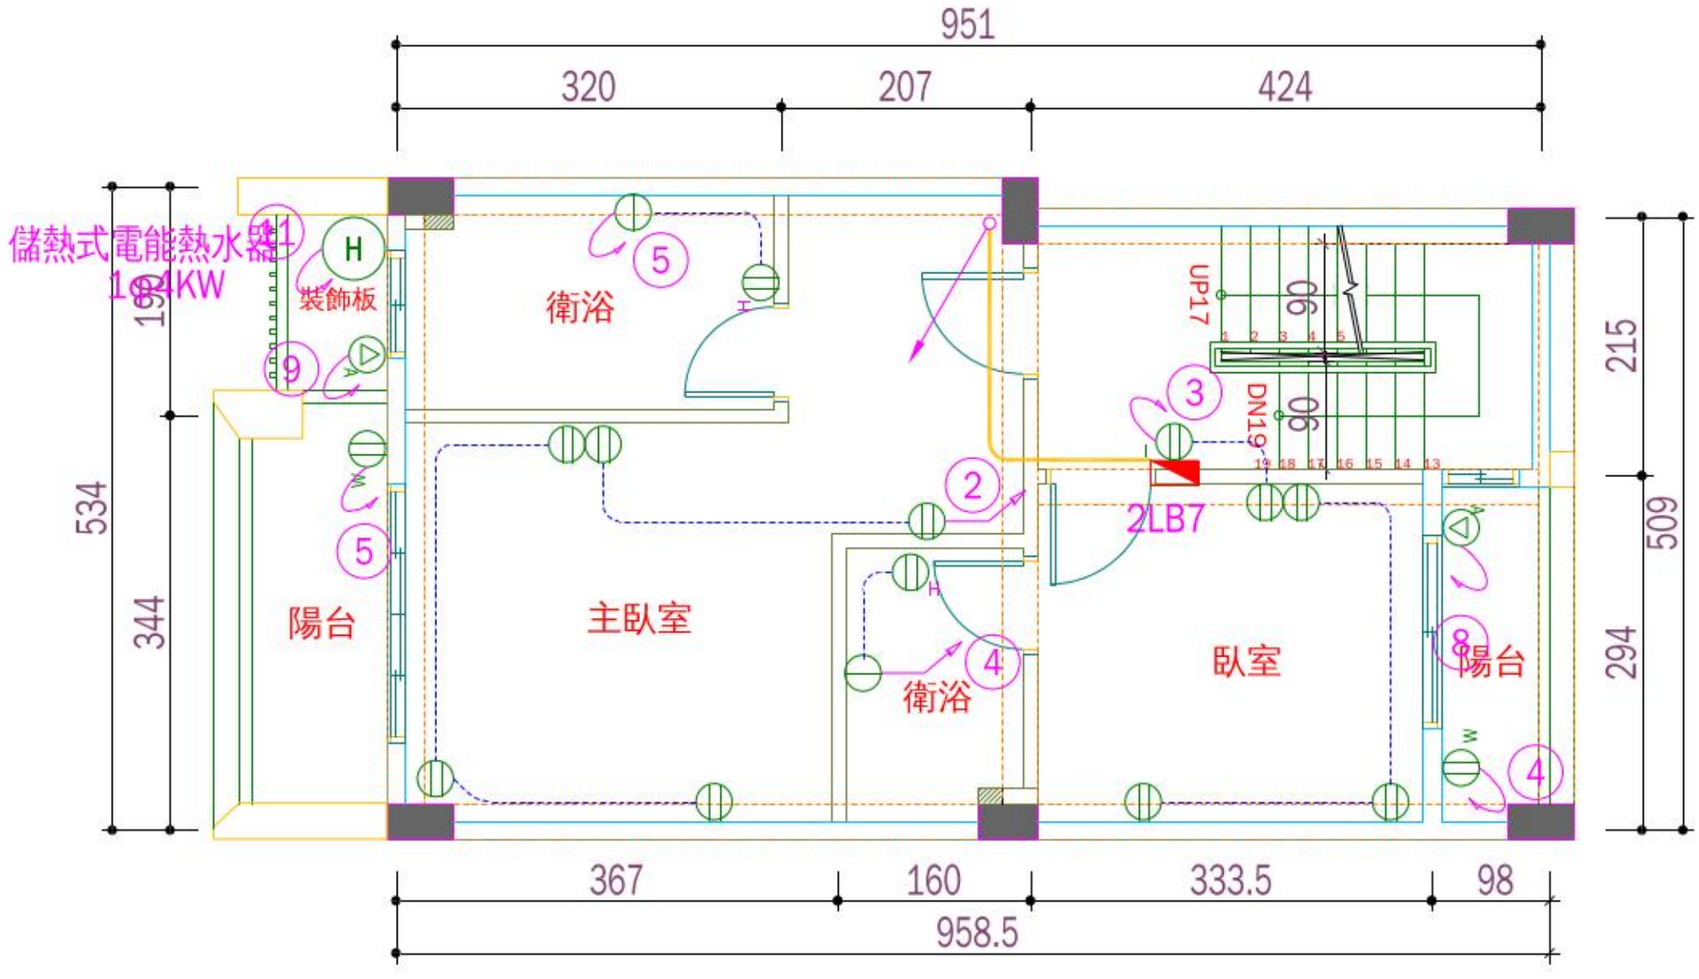

2F插座設備配置圖

S=1/100

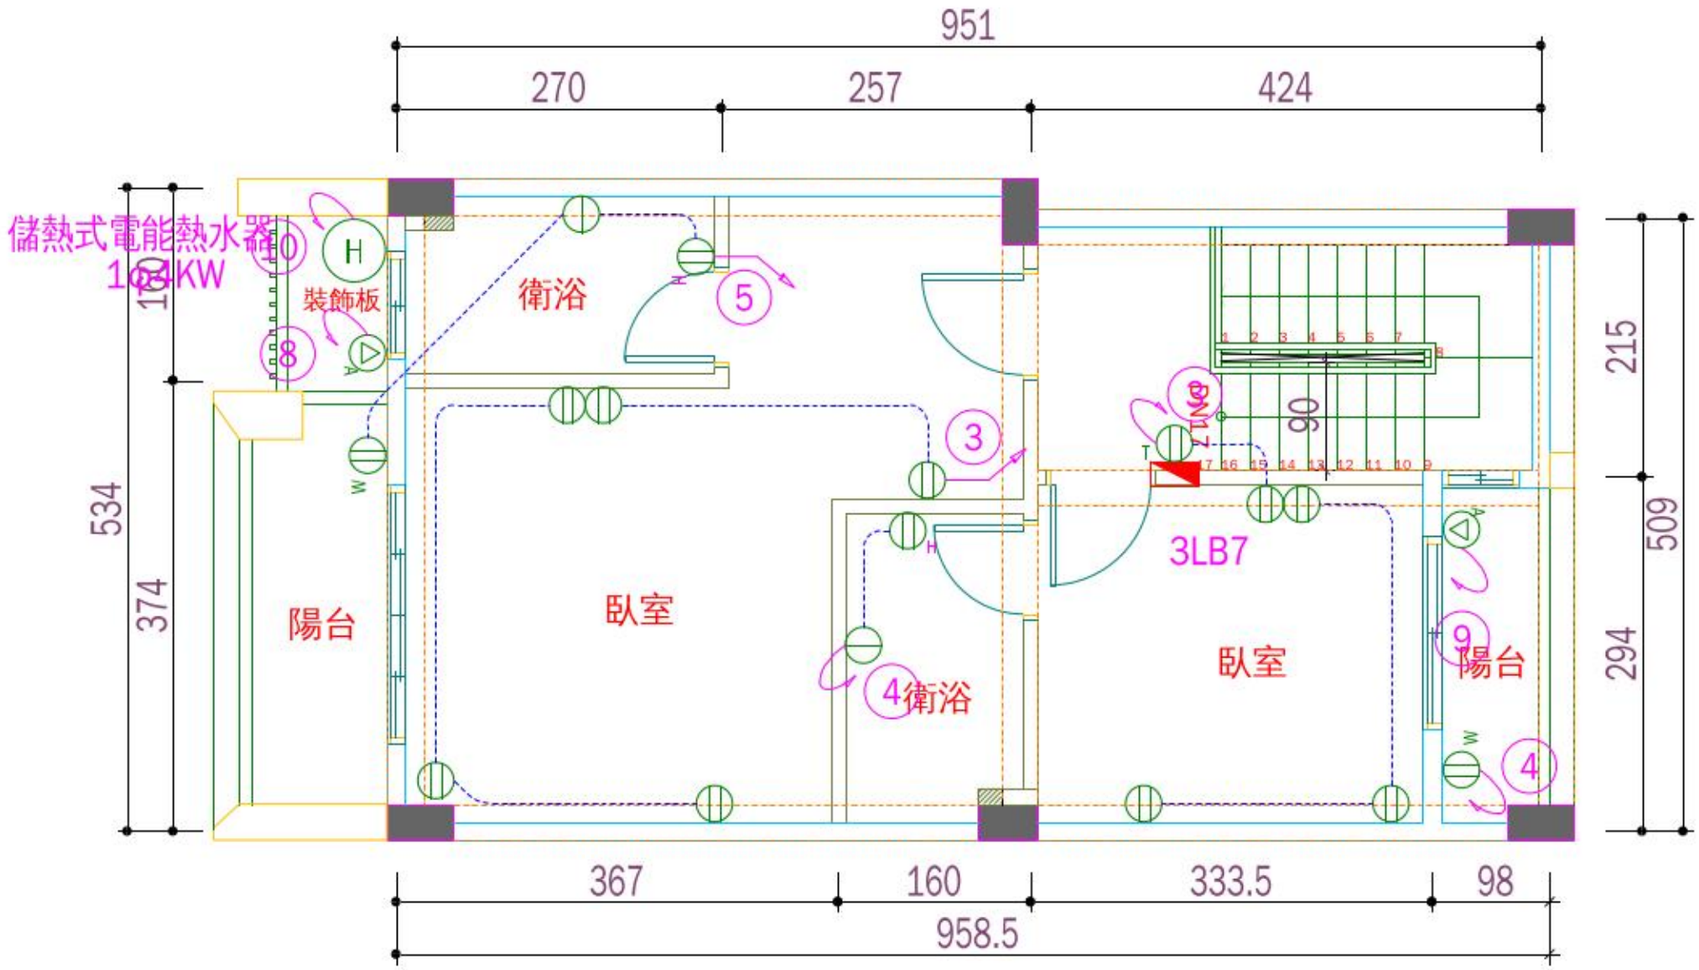


3F插座設備配置圖

S=1/100

圖例表 — 插座設備配置圖


圖例	名稱	說明	數量
◍	雙插座	旁註W/K/A/T/H依原圖標示	41
◑	單插座	旁註字母依原圖標示	8
◬	專用插座	專用回路	8
Ⓗ	電熱水器專用出線口	容量依註記	2
Ⓜ	電動機出線口(揚水泵)	容量依註記	1
Ⓙ	接線盒(出線匣)		2
◥	電燈分電盤	盤名依註記(如1LB7)	3
⊠	電度表(電表箱)	戶號依註記	1
⏚	接地	依原圖註記	1
◯	迴路編號	數字為分路編號，箭頭指向分電盤	28
----------	插座分路配線	線徑/管徑依單線圖	
————	幹線	電表至分電盤，規格依單線圖	
----------	接地線	接至接地極	

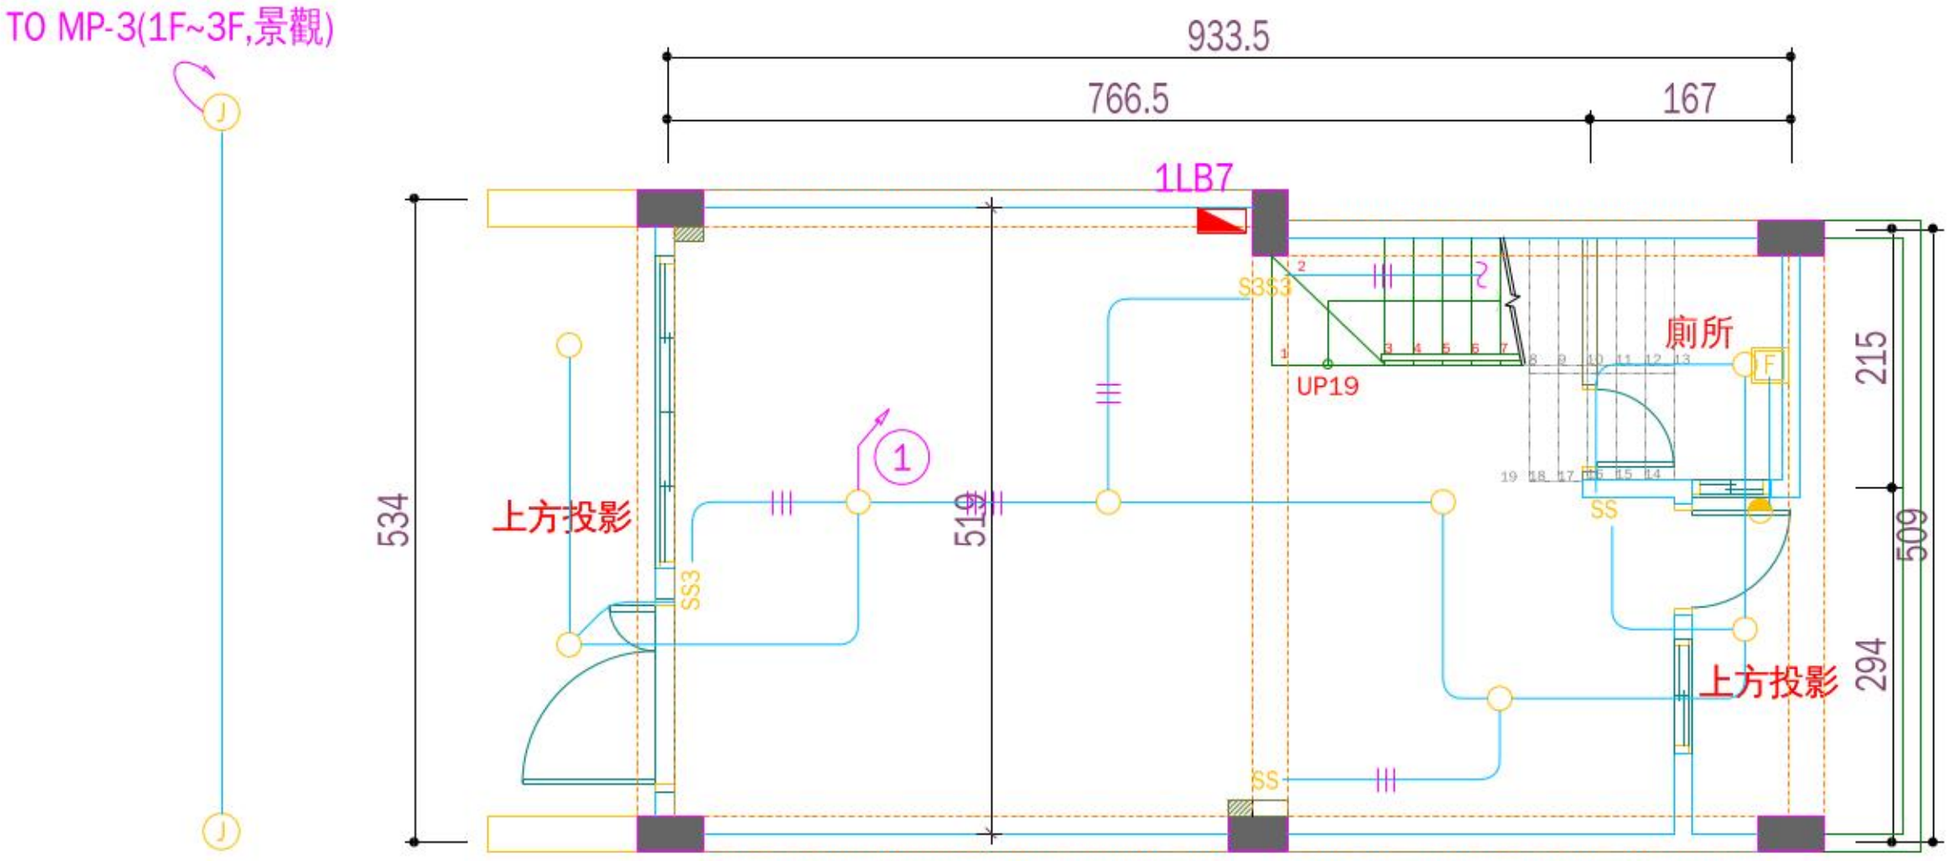

1F照明設備配置圖


S=1/100

TO MP-3(1F~3F,景觀)

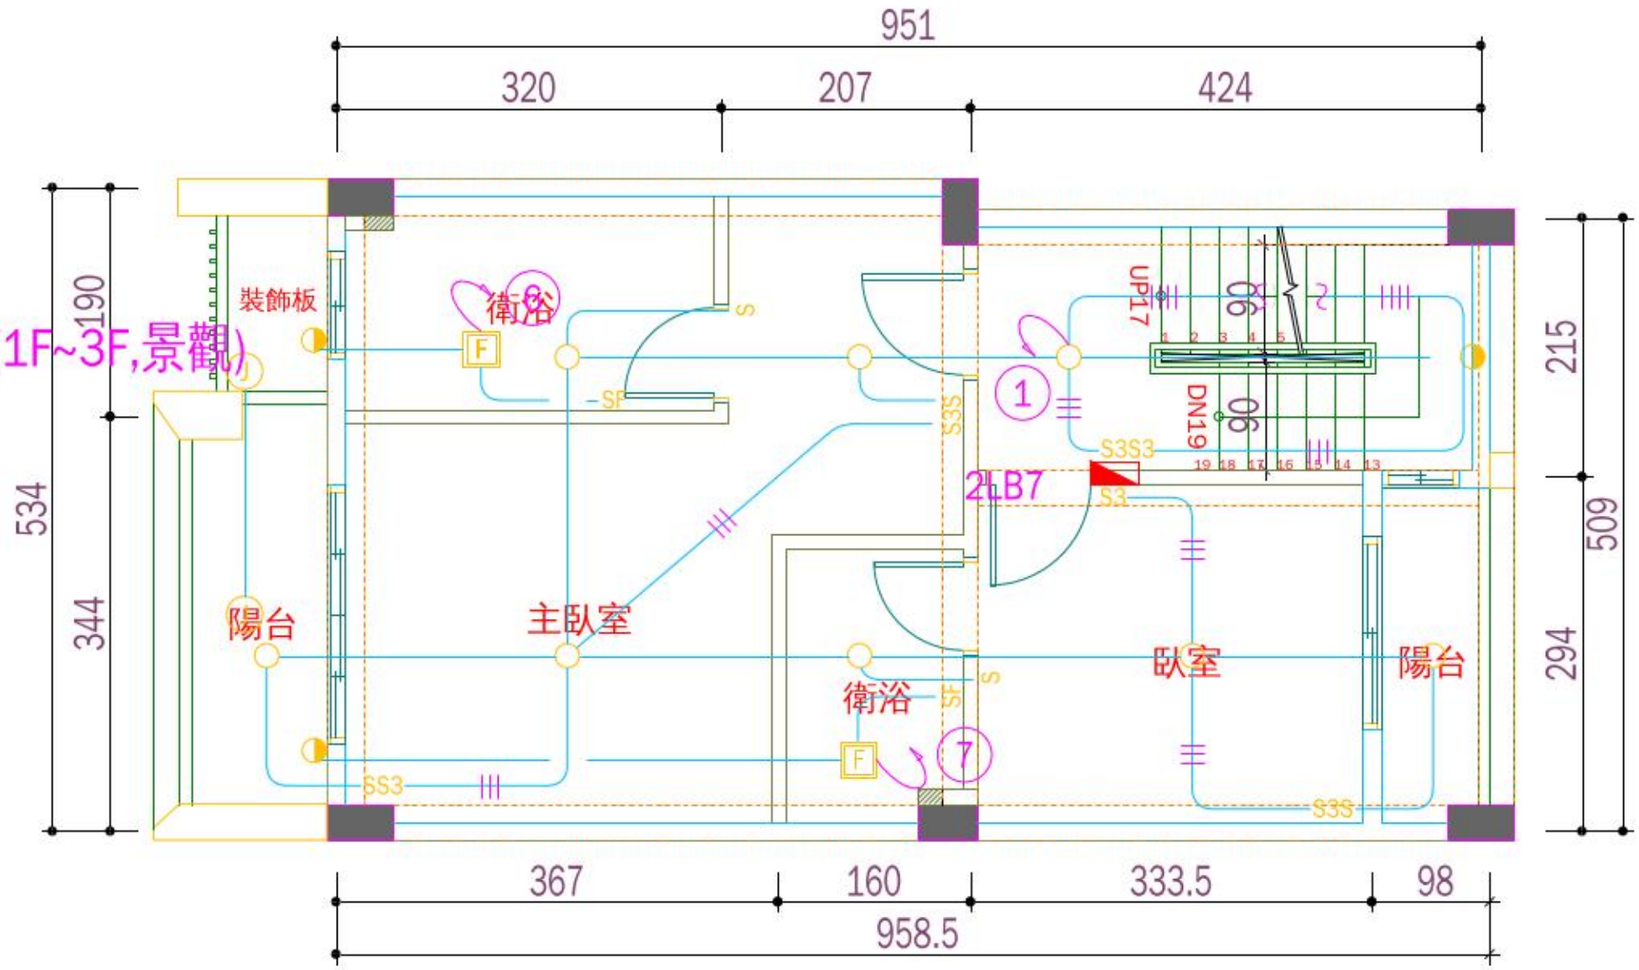

2F照明設備配置圖

S=1/100

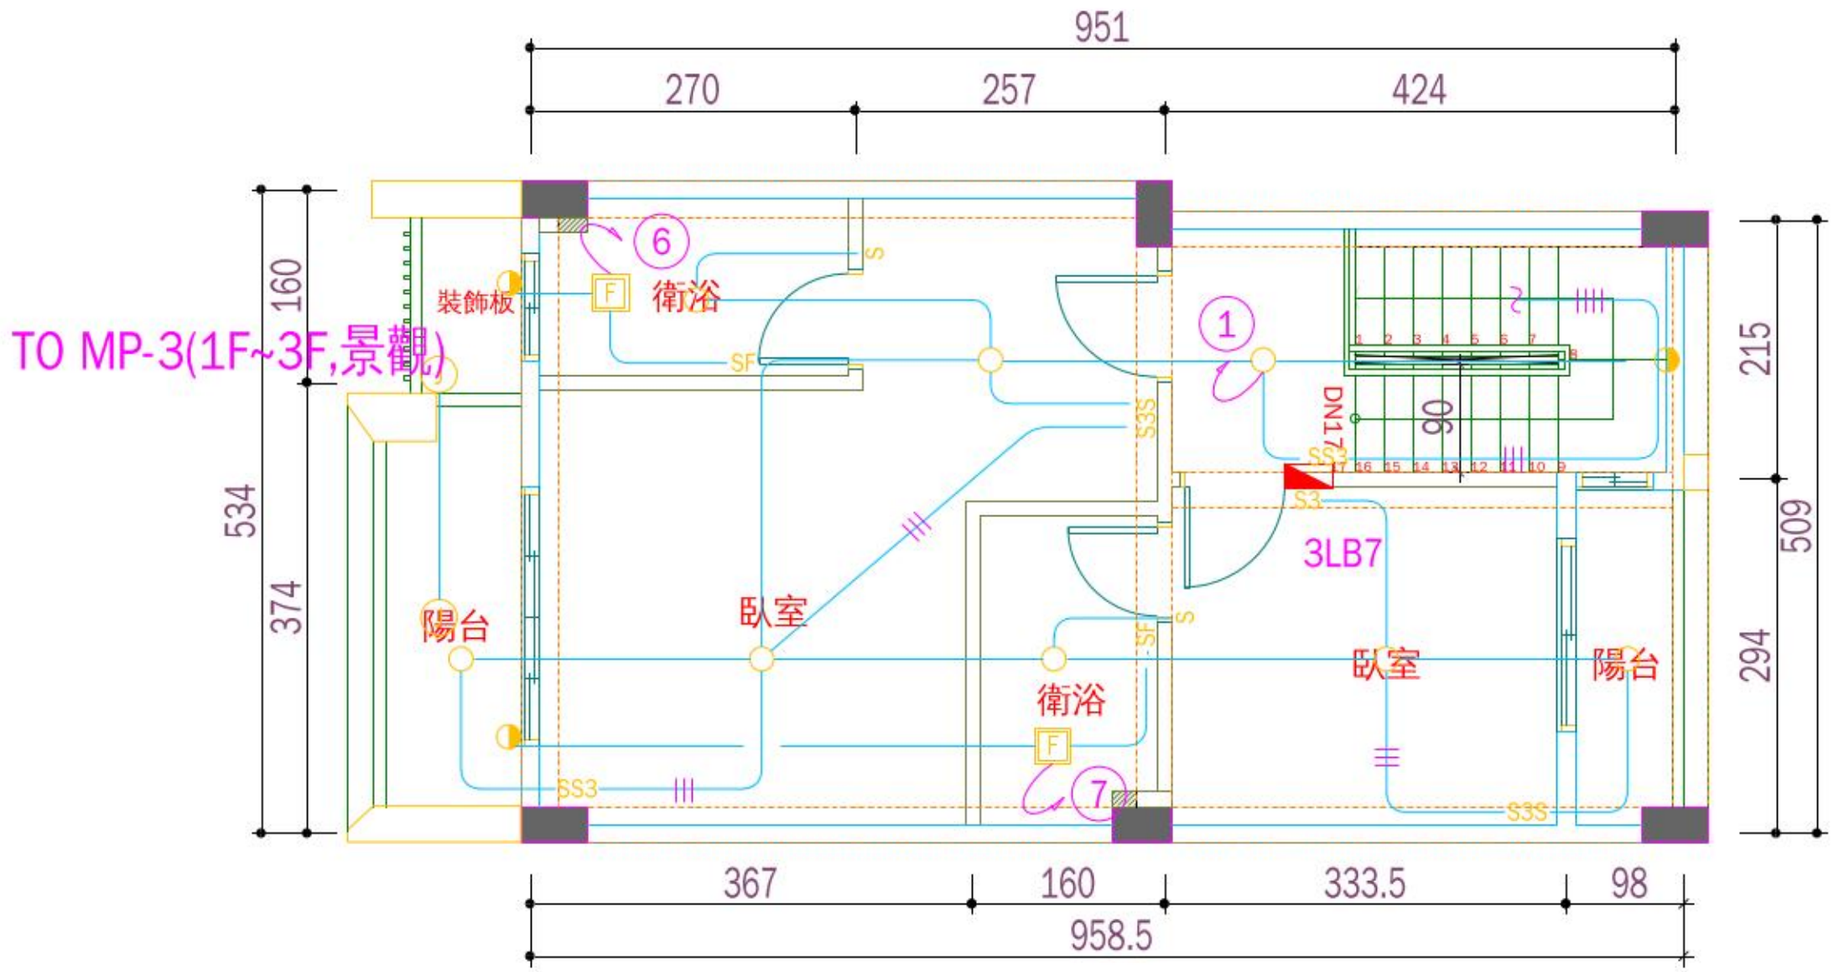


3F照明設備配置圖

S=1/100


圖例表 — 照明設備配置圖

圖例	名稱	說明	數量
○	燈具出線口(吸頂燈)	燈具型式依室內設計	24
◑	壁燈		7
F	排風機		5
J	接線盒(景觀照明)		6
	開關	S:單切 S3:三路 SF:排風機，多字為多連	22
	電燈分電盤	盤名依註記(如1LB7)	3
	迴路編號	數字為分路編號，箭頭指向分電盤	7
	照明分路配線	短劃數為導線根數，線徑/管徑依單線圖	

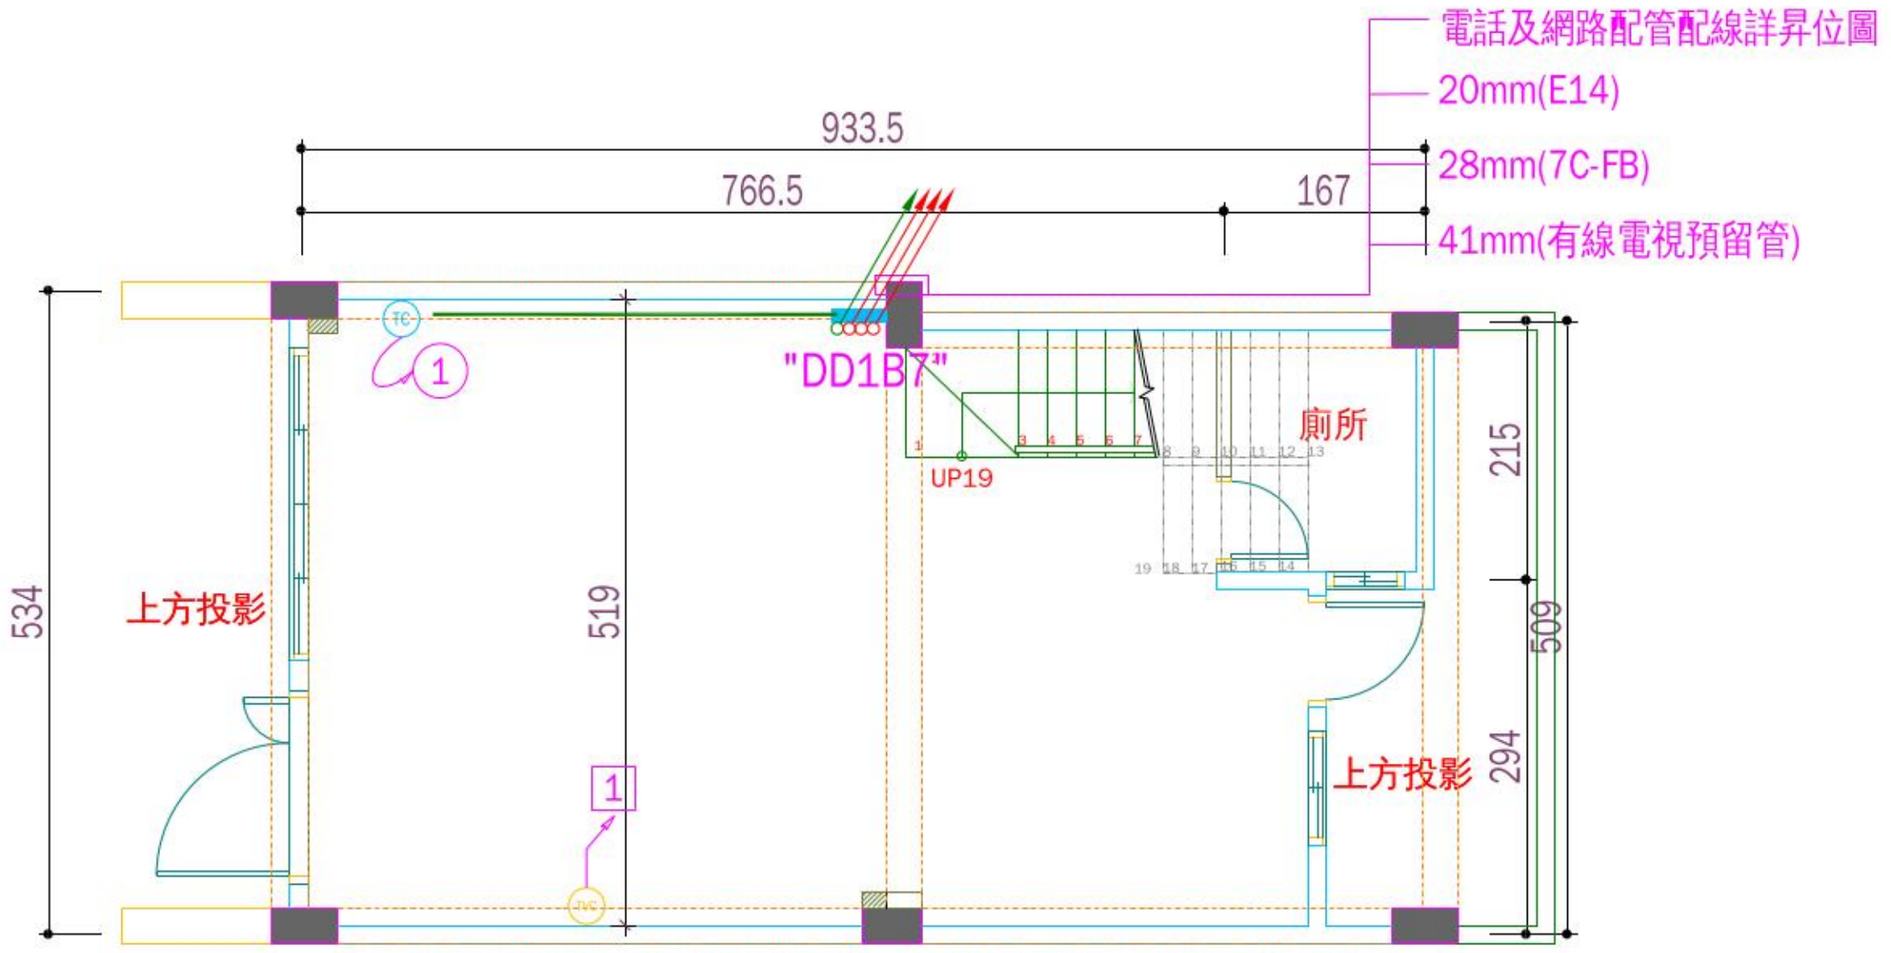


1F電信設備配置圖

S=1/100

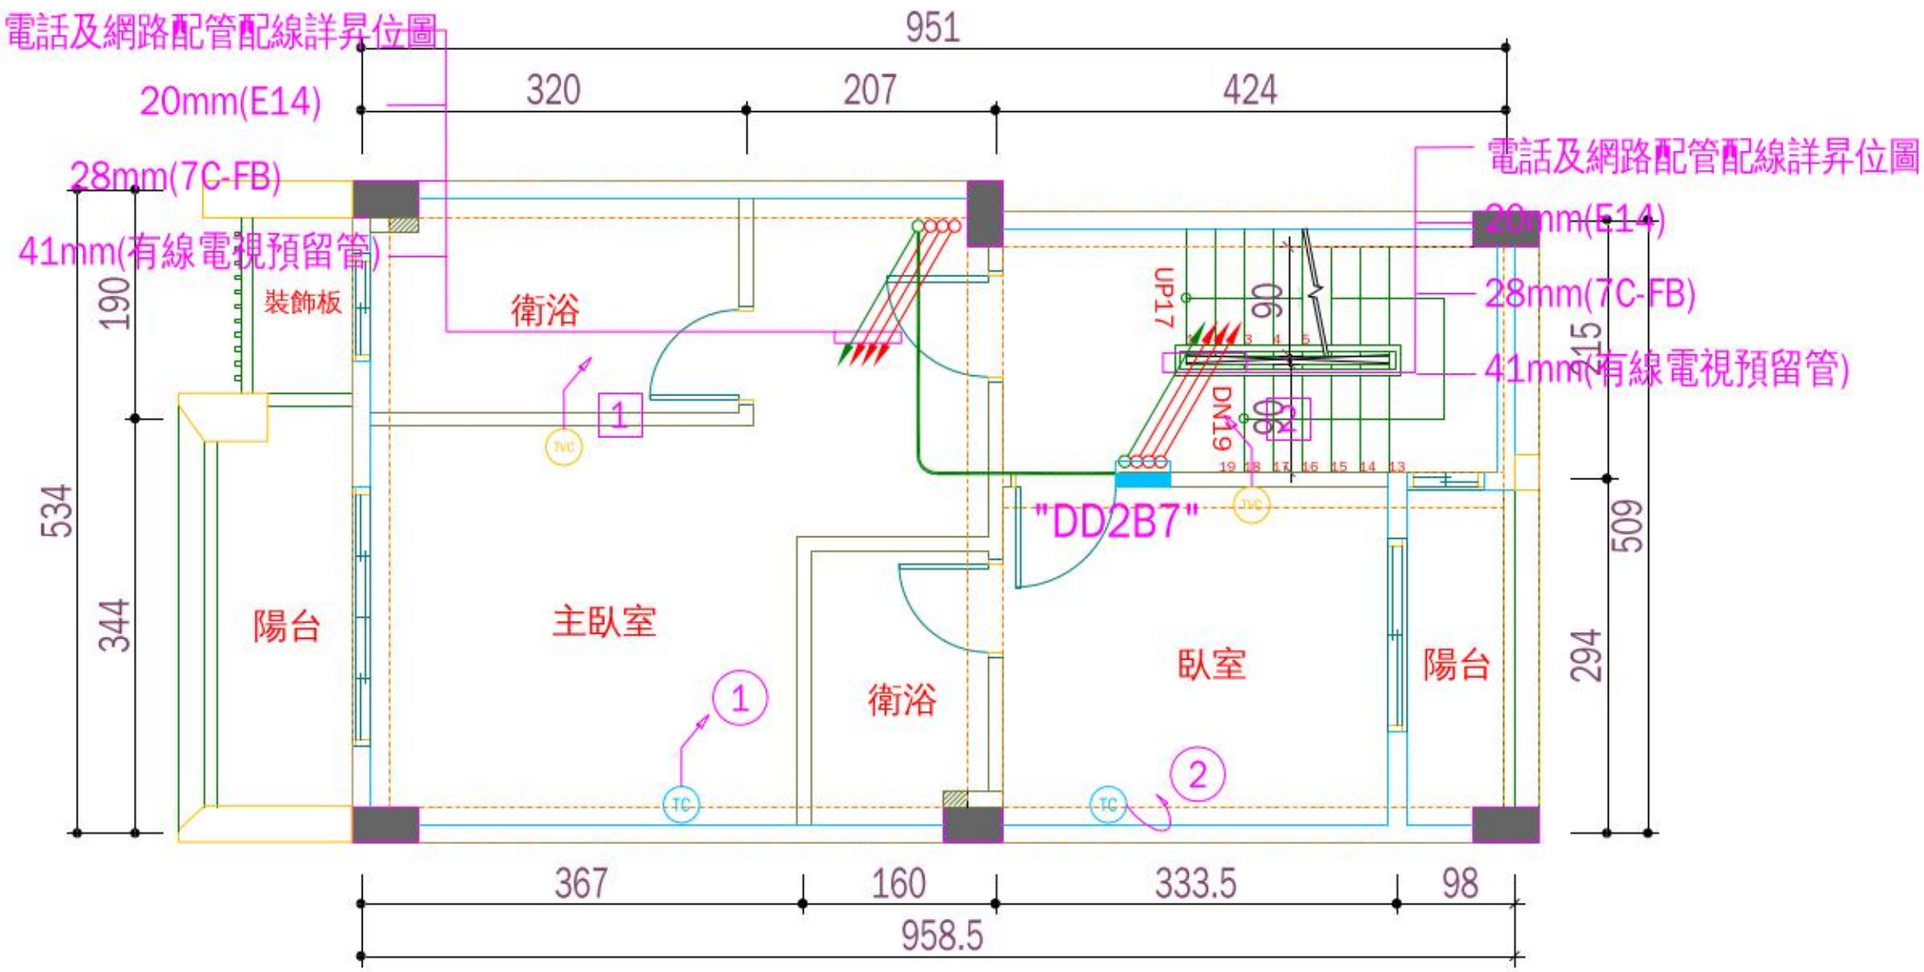

2F電信設備配置圖

S=1/100

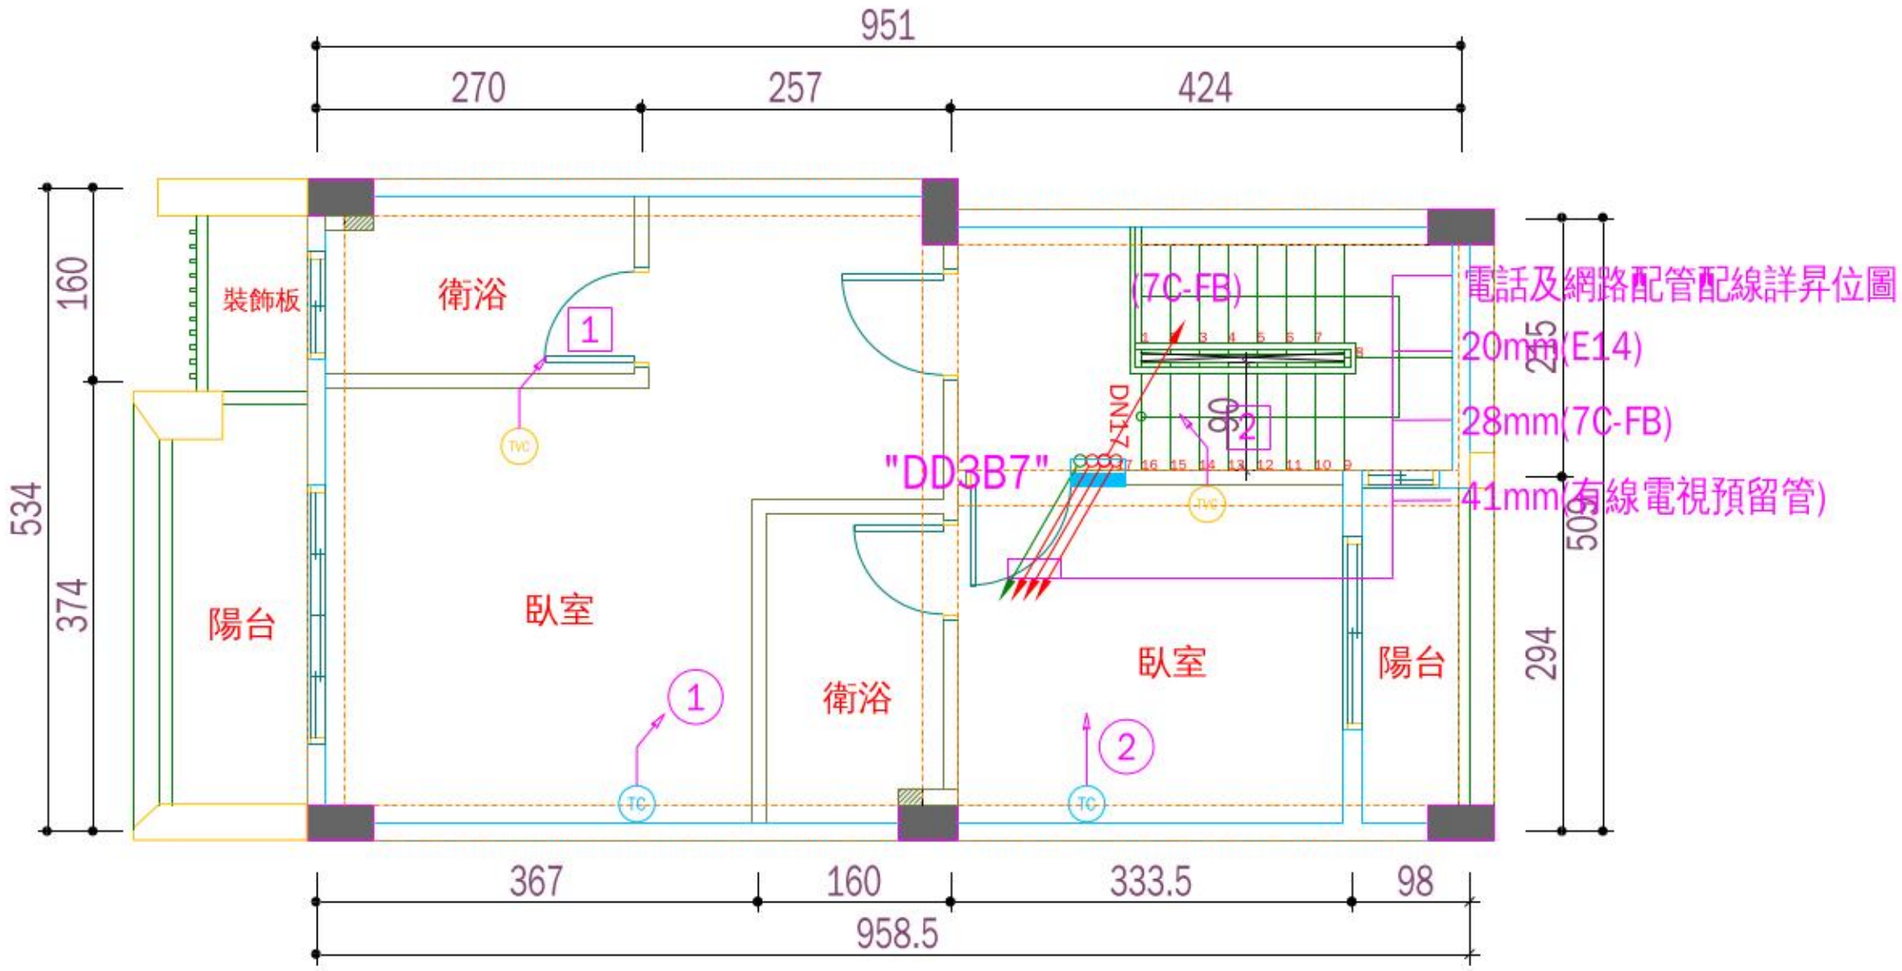


3F電信設備配置圖

S=1/100


圖例表 — 電信設備配置圖

圖例	名稱	說明	數量
TC	電信出線口(TC)	電話/網路	5
TVC	有線電視出線口(TVC)		5
	電信箱	箱名依註記(如DD1B7)	3
	出線口編號(圓)	電信出線口編號	5
	出線口編號(方)	有線電視出線口編號	5
	電話/網路配管	20mm(E14)、28mm(7C-FB)，詳昇位圖	
	有線電視配管	41mm 有線電視預留管，詳昇位圖	

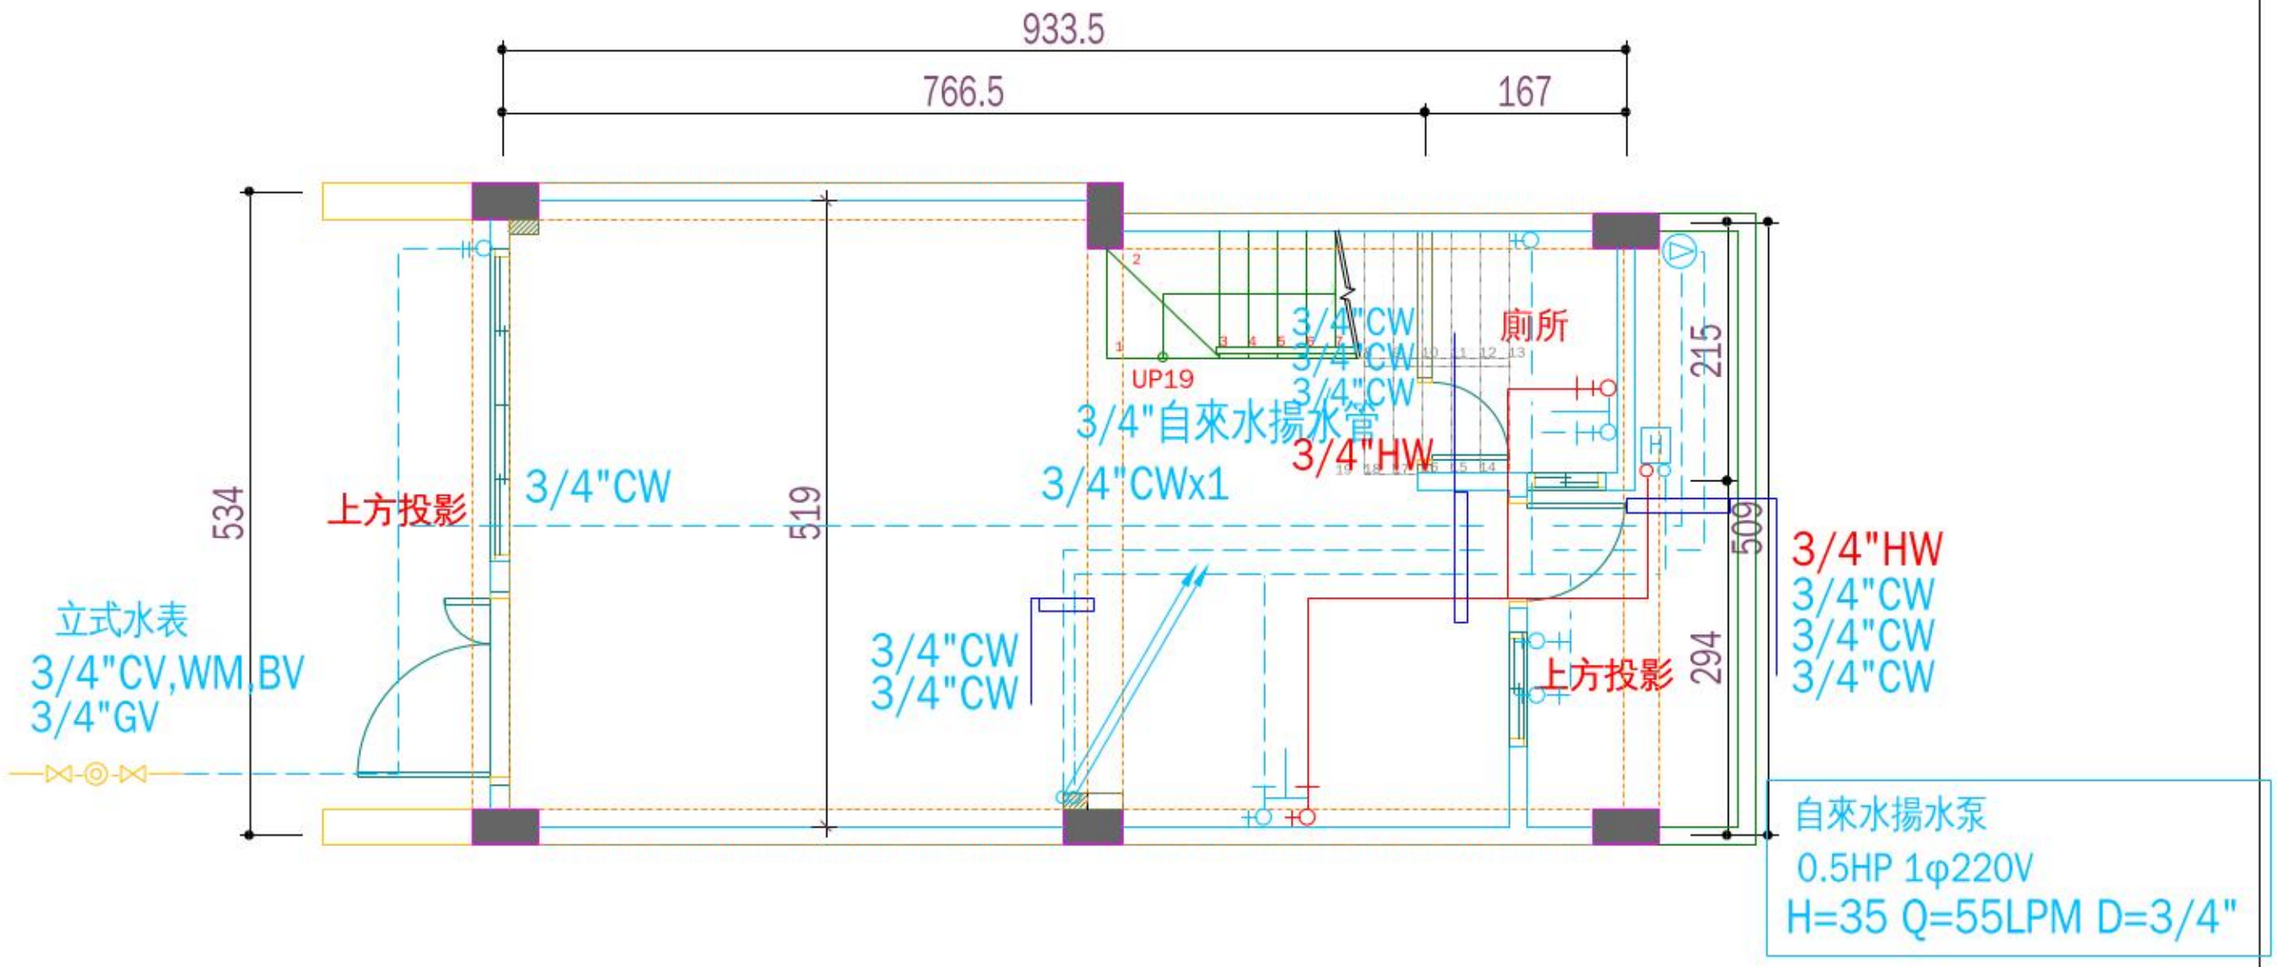


1F給水設備配置圖

S=1/100

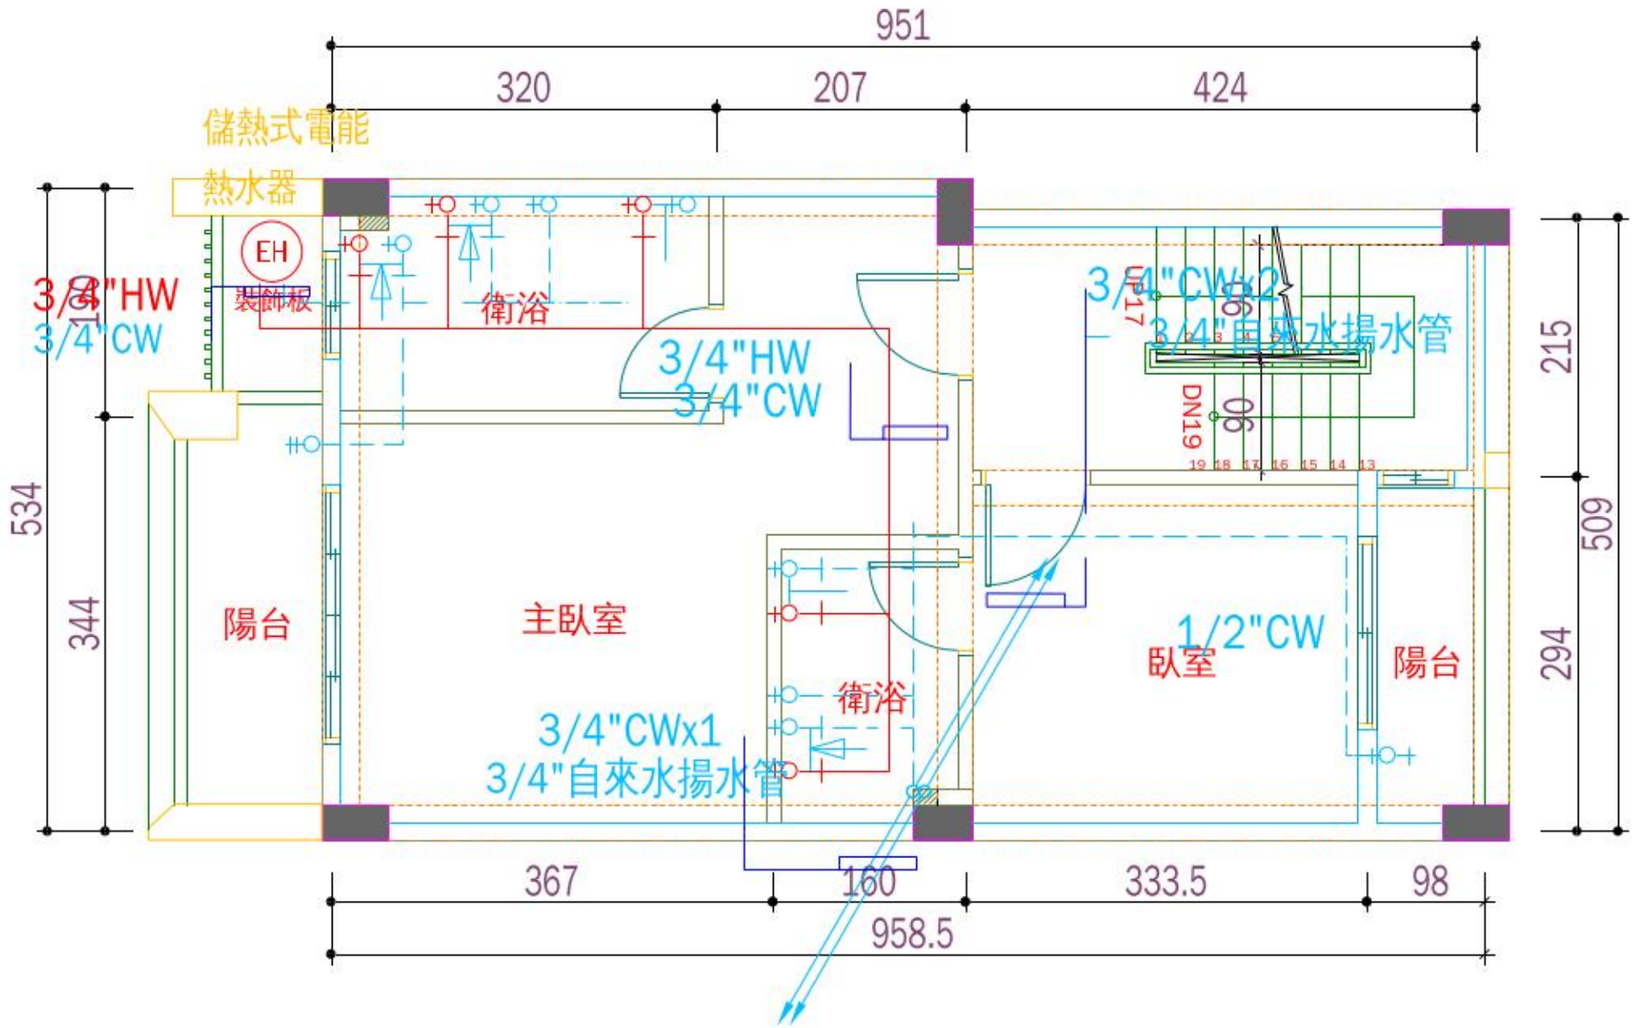

2F給水設備配置圖

S=1/100

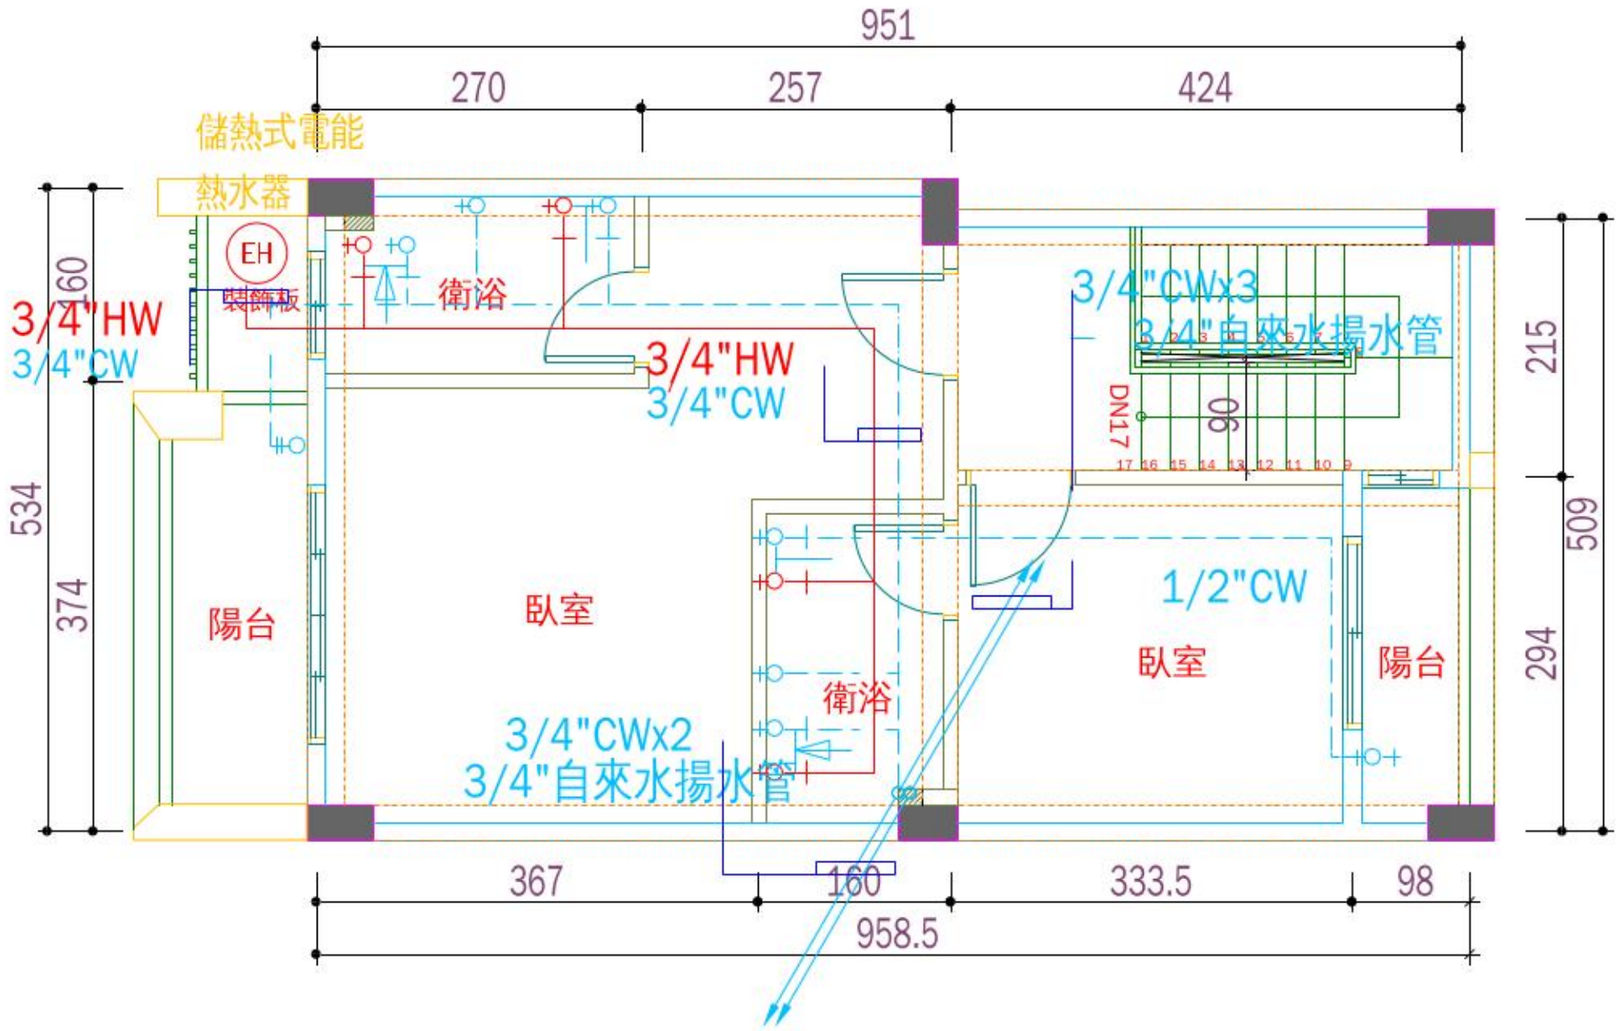


3F給水設備配置圖

S=1/100


圖例表 — 給水設備配置圖

圖例	名稱	說明	數量
+○	給水栓/器具給水出口	冷水(CW)藍、熱水(HW)紅	34
EH	儲熱式電能熱水器	1φ220V 4KW	2
H	電熱水器(廚下/小型)		1
⋈	閥件(GV/CV/BV)	水表組：3/4"CV,WM,BV + 3/4"GV	2
◎	水表(WM)		1
▷	加壓/揚水泵	容量依註記	1
———	冷水管(CW)	管徑依註記	
———	熱水管(HW)	管徑依註記	
———	穿樑/穿版套管		

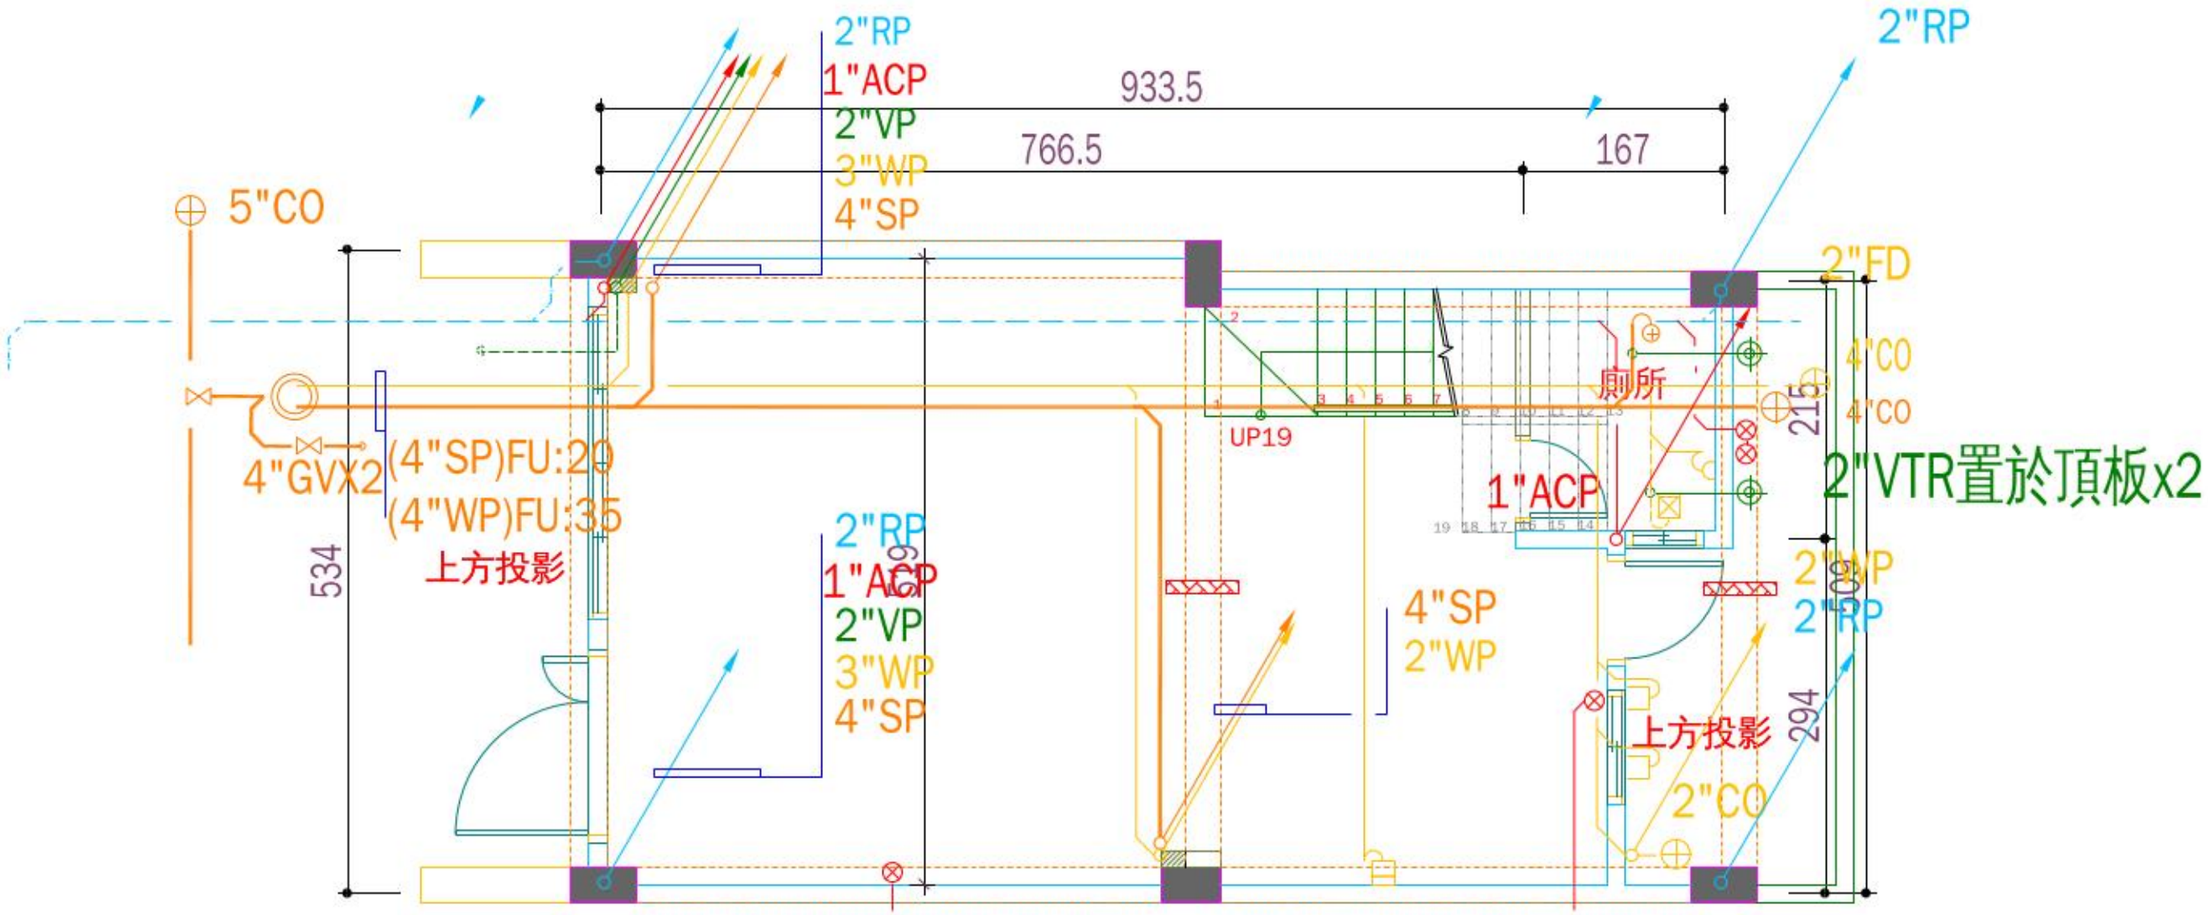


1F排水設備配置圖

S=1/100

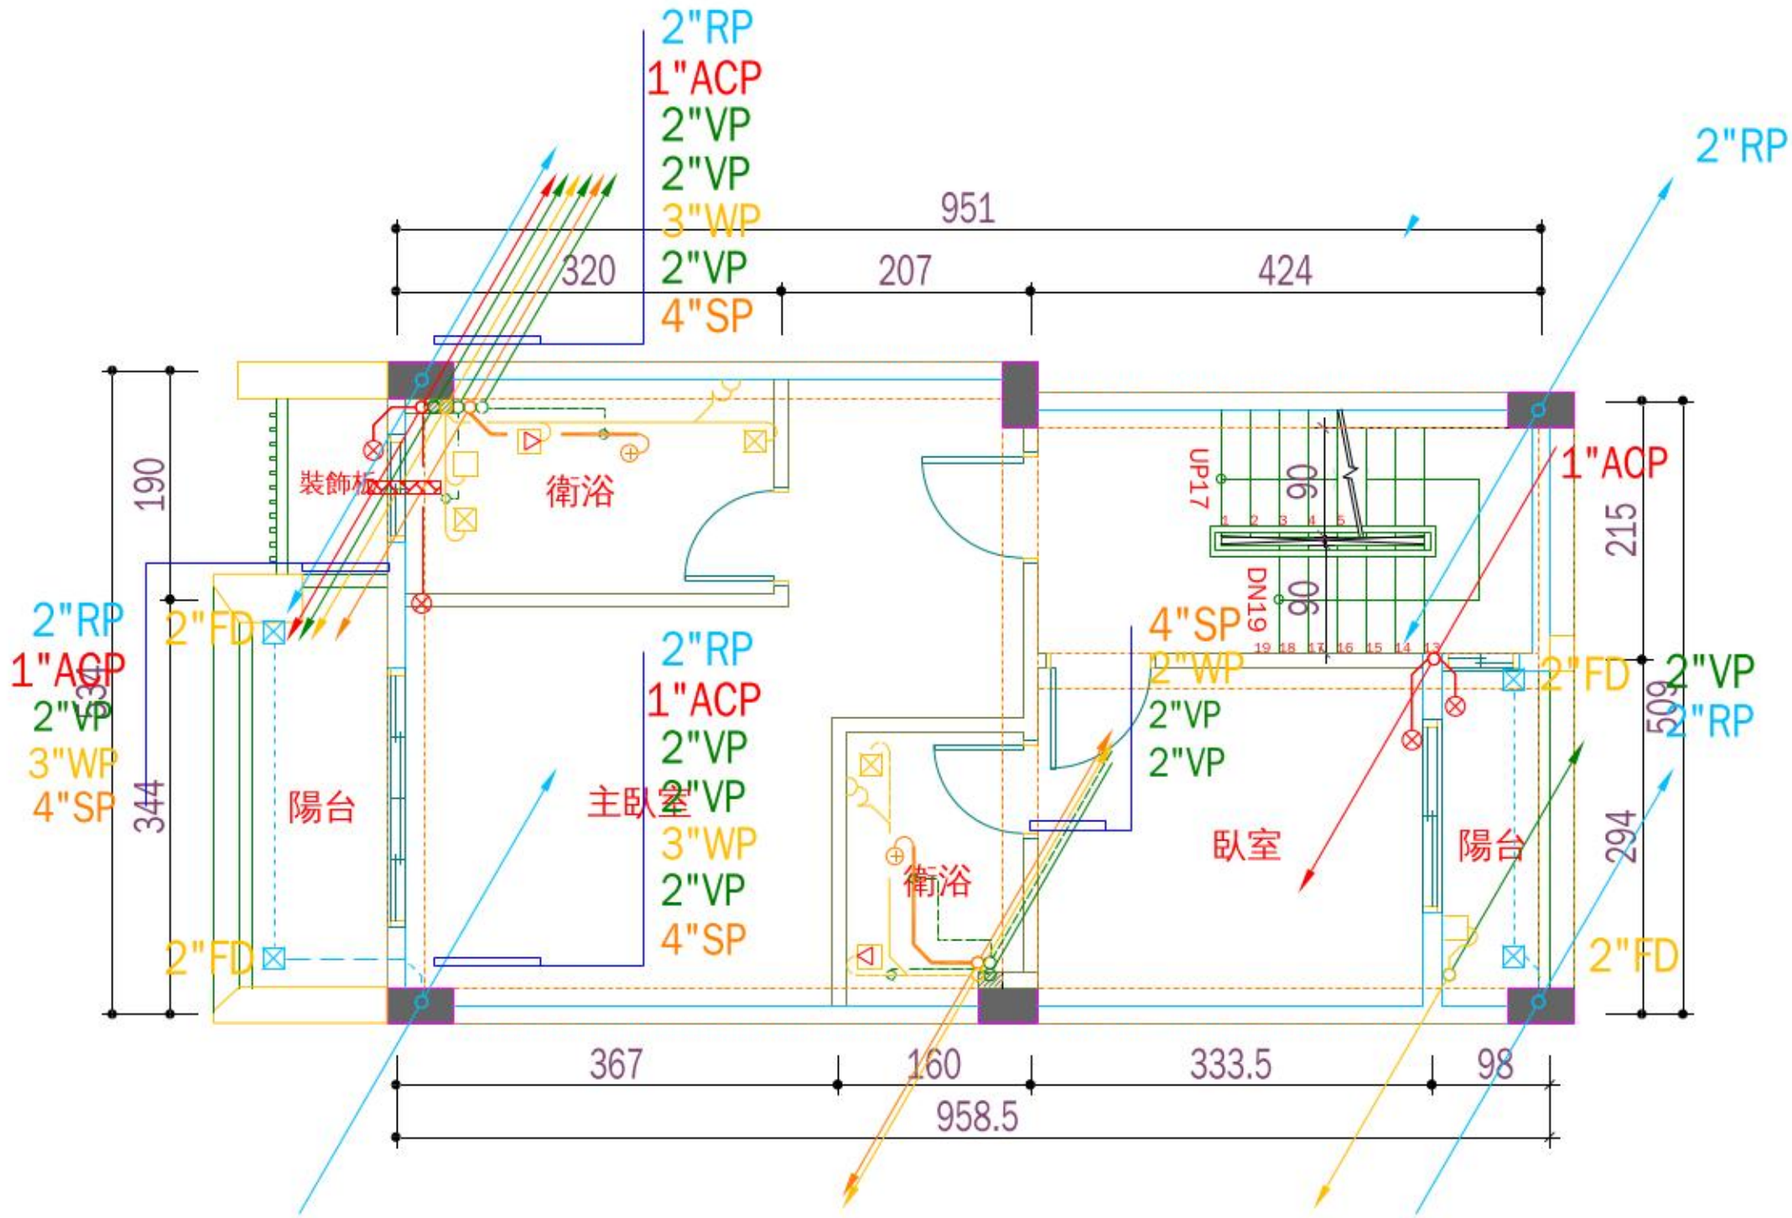

2F排水設備配置圖

S=1/100

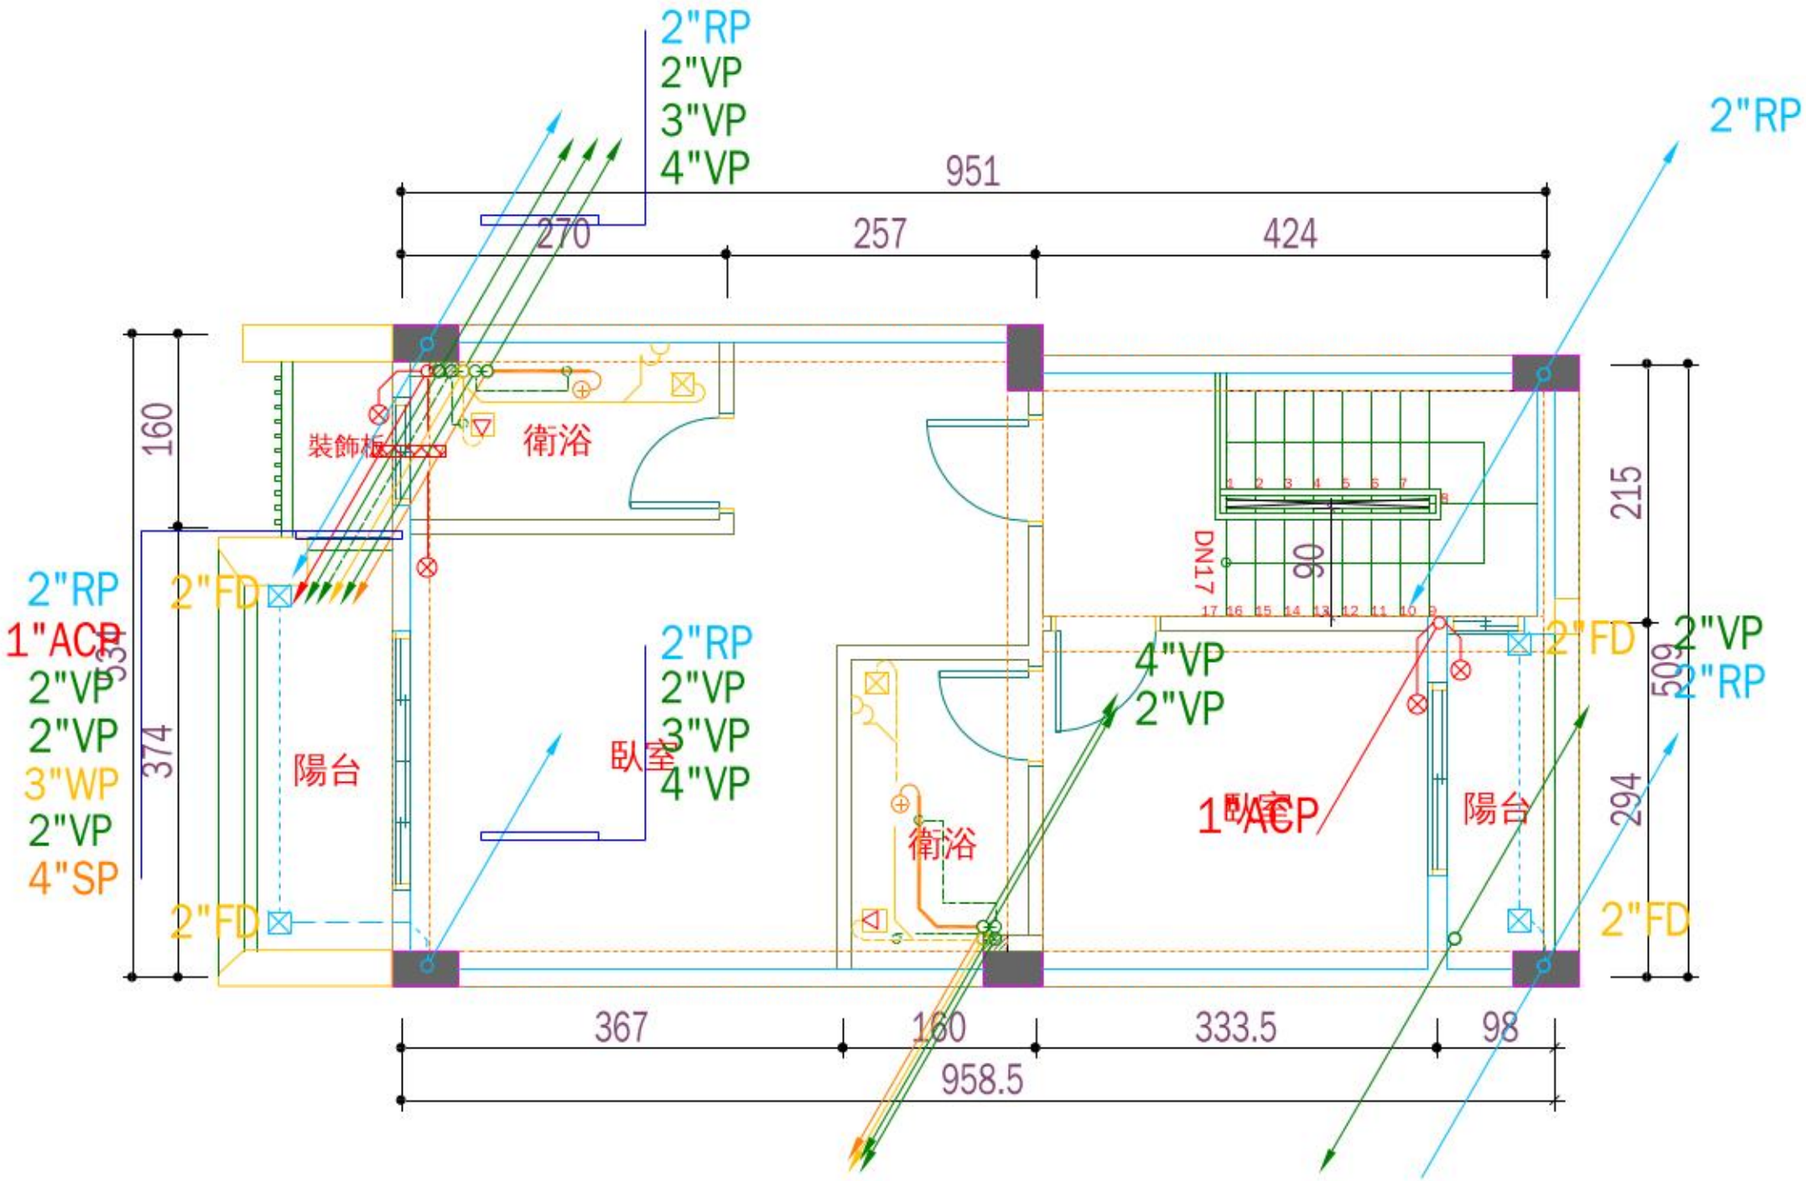

3F排水設備配置圖

S=1/100

圖例表 — 排水設備配置圖

圖例	名稱	說明	數量
⊠	地板落水頭(FD)	陽台(雨水)青色、浴室(雜排水)黃色	14
⊕	清潔口(CO)	管徑依註記	4
⊗	冷氣排水口(ACP)		12
⊕	馬桶排水口	接汙水管SP	5
◎	排水陰井	4"SP FU:20、4"WP FU:35	1
⋈	閘閥(GV)		2
⊕	通氣管出屋頂(VTR)	置於頂板	2
———	汙水管(SP)	管徑依註記	
———	雜排水管(WP)	管徑依註記	
———	通氣管(VP)	管徑依註記	
———	雨水管(RP)	管徑依註記	
———	冷氣排水管(ACP)	管徑依註記	